



**Общество с ограниченной ответственностью  
«Альянс Энерджи»**

Юр. адрес: 400074, г. Волгоград, ул. Баррикадная, 1, корпус 7, офис 6  
ИНН 3445123098, КПП 344501001, ОГРН 1123460001390  
Р/с № 40702810503100001142 ПАО КБ "ЦЕНТР-ИНВЕСТ" ФИЛИАЛ № 9,  
к/с 30101810100000000870, БИК 041806870  
E-mail: mail@allnrg.ru, тел. (8442) 56-44-34



## Концептуальный проект

Разработка проектных решений по капитальному ремонту 2-го этажа  
и инженерных систем бытовых помещений ЦРМО РМО отд. №2.

УТВЕРЖДАЮ:

Зам. главного инженера по ремонту  
АО "Корпорация Красный Октябрь"

\_\_\_\_\_ Захаров Я.И.

СОГЛАСОВАНО:

Начальник УКС  
АО "Корпорация Красный Октябрь"

\_\_\_\_\_ Камчатников П.Е.

СОГЛАСОВАНО:

Начальник ЦРМО РМО отд. №2.  
АО "Корпорация Красный Октябрь"


\_\_\_\_\_ Маслов В.А.

Концептуальный проект разработан  
ООО "Альянс Энерджи"

Архитектор: Несмиянов Л.И. \_\_\_\_\_

Директор: Злобин В.М. \_\_\_\_\_

**Волгоград - 2022**

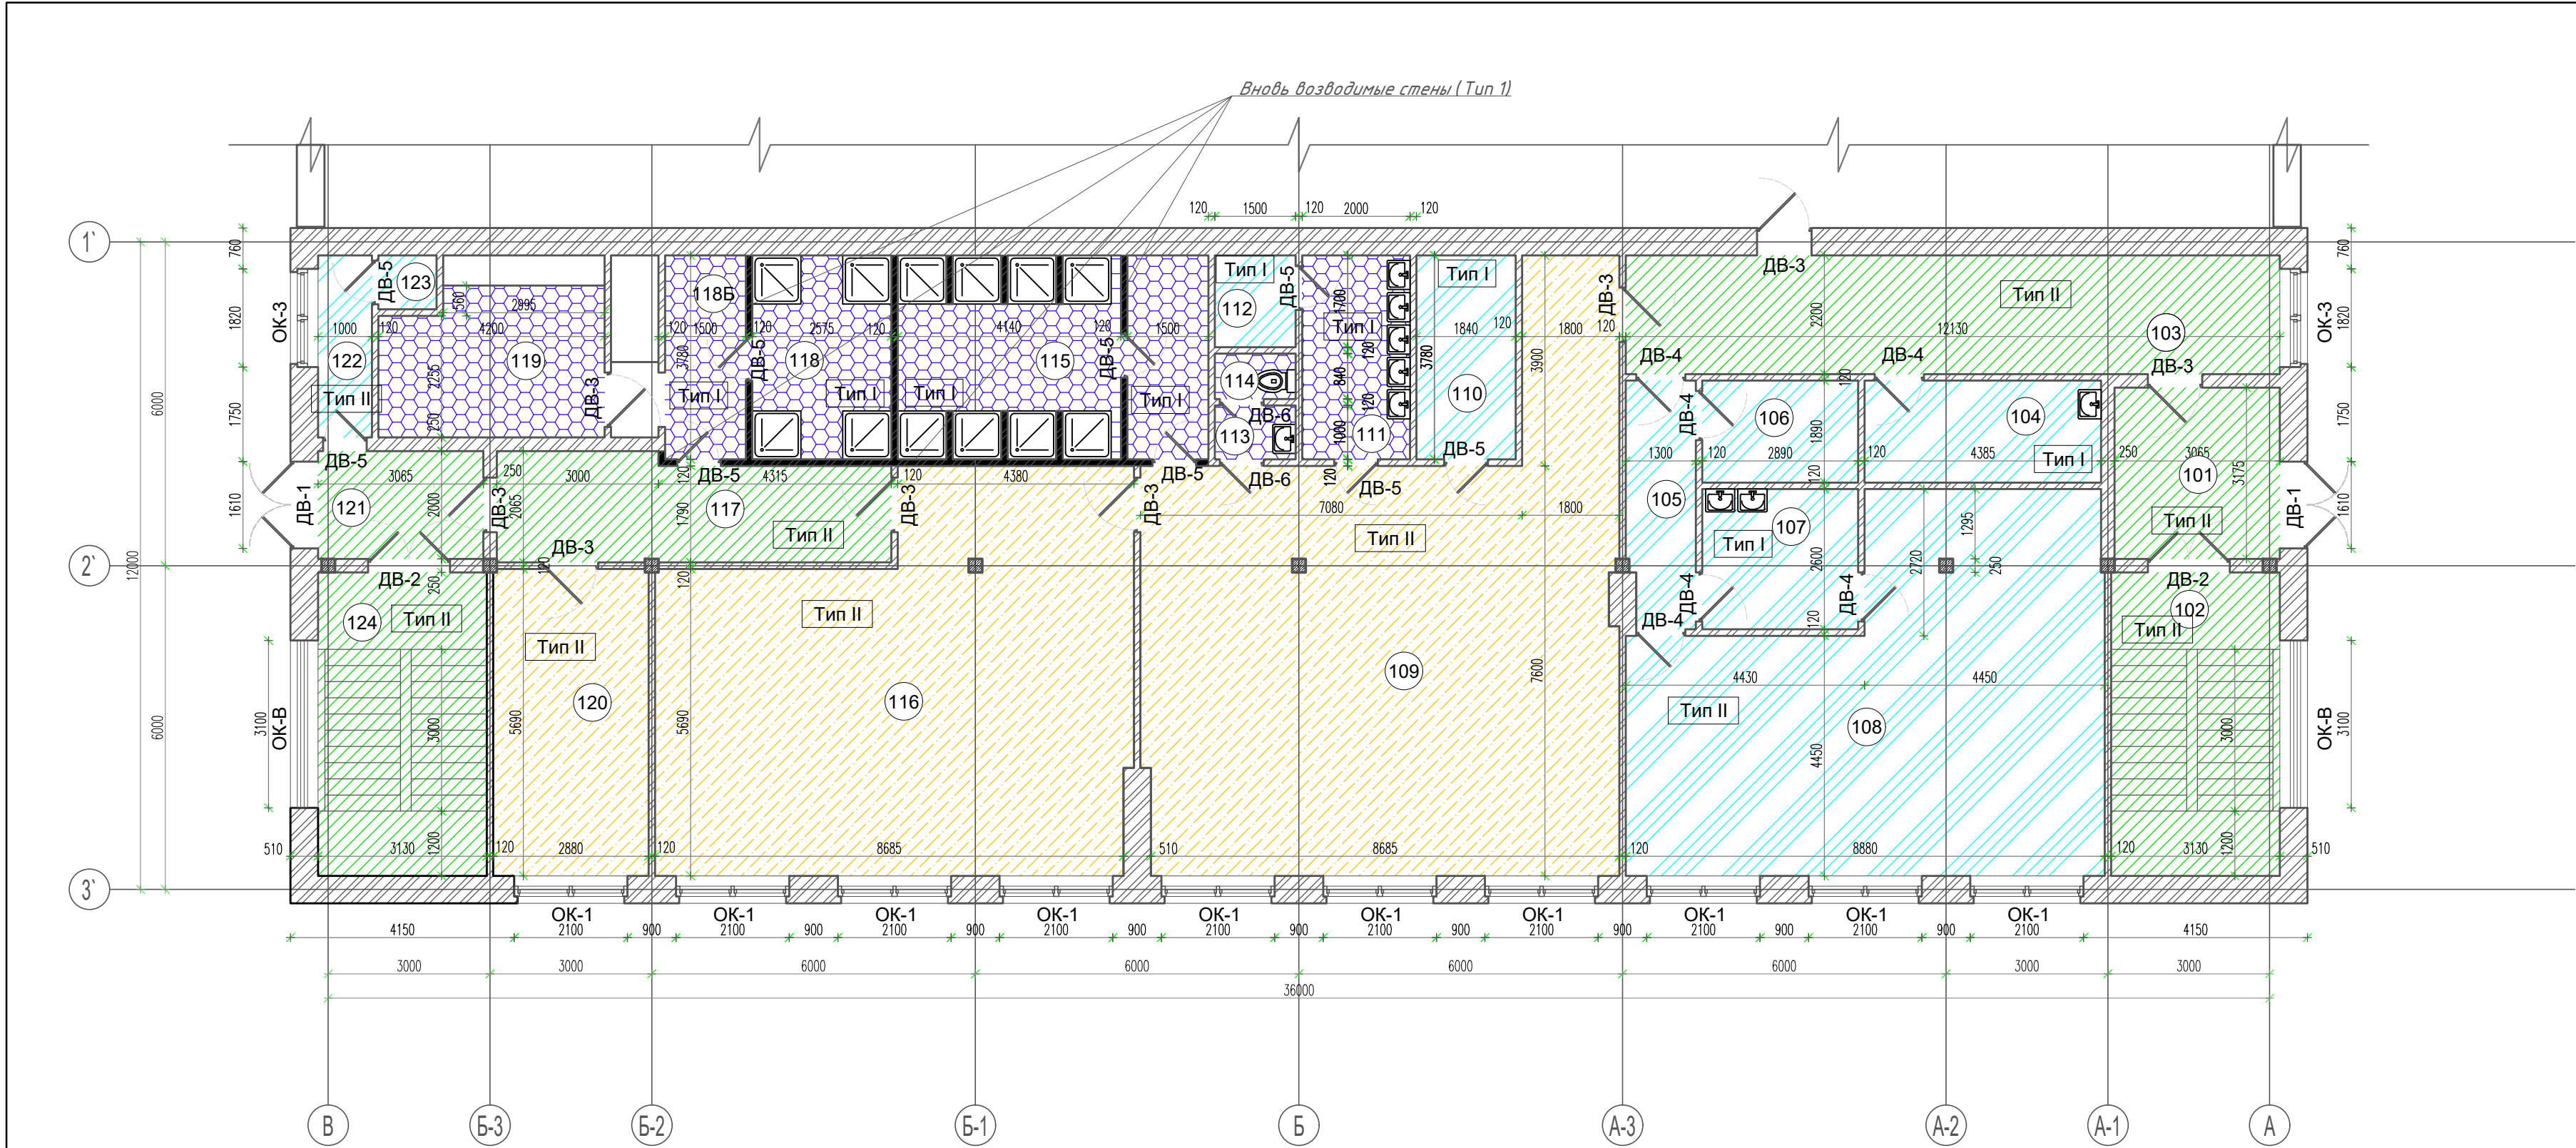

Зонирование

- Зона кабинетов и офисных помещений
- Зона коридоров и лестниц
- Зона раздевалок
- Зона помещений с мокрыми процессами
- Зона вспомогательных помещений
- Тип II Тип покрытия пола

Экспликация помещений


| Номер | Наименование помещения  | Площадь |  |
|-------|-------------------------|---------|--|
| 101   | Тамбур                  | 9.73    |  |
| 102   | Лестничная клетка       | 17.61   |  |
| 103   | Коридор                 | 26.69   |  |
| 104   | Помещение               | 8.29    |  |
| 105   | Коридор                 | 5.77    |  |
| 106   | Помещение               | 5.46    |  |
| 107   | Помещение               | 7.51    |  |
| 108   | Помещение приема пищи   | 51.52   |  |
| 109   | Раздевалка женская      | 73.91   |  |
| 110   | Техническое помещение   | 6.96    |  |
| 111   | Помещение рукомоичников | 7.56    |  |
| 112   | Техническое помещение   | 2.55    |  |
| 113   | Тамбур С/У              | 1.50    |  |
| 114   | С/У                     | 1.26    |  |
| 115   | Душевые с тамбуром      | 20.77   |  |
| 116   | Тренажерный зал         | 58.50   |  |
| 117   | Коридор                 | 13.90   |  |
| 118   | Душевые с тамбуром      | 15.50   |  |
| 118Б  | Купель                  | 5.67    |  |
| 119   | Сауна                   | 11.14   |  |
| 120   | Комната отдыха          | 16.38   |  |
| 121   | Тамбур                  | 6.13    |  |
| 122   | Коридор                 | 3.37    |  |
| 123   | Тех. помещение          | 1.08    |  |
| 124   | Лестничная клетка       | 17.61   |  |
| Всего |                         | 390.69  |  |

|          |      |      |        |         |      |                                                                                      |  |                      |      |        |
|----------|------|------|--------|---------|------|--------------------------------------------------------------------------------------|--|----------------------|------|--------|
|          |      |      |        |         |      | 03-2022/4 АР                                                                         |  |                      |      |        |
|          |      |      |        |         |      | Капитальный ремонт инженерных систем здания и бытовых помещений<br>ЦРМО РМО отд. №2. |  |                      |      |        |
| Изм.     | Кол. | Лист | № док. | Подпись | Дата |                                                                                      |  |                      |      |        |
| ГАП      |      |      |        |         |      | Ремонт бытового корпуса                                                              |  | Стадия               | Лист | Листов |
| Н.контр. |      |      |        |         |      |                                                                                      |  |                      |      |        |
|          |      |      |        |         |      | План 1 этажа                                                                         |  | 000 "Альянс Энерджи" |      |        |
|          |      |      |        |         |      |                                                                                      |  |                      |      |        |



Экспликация помещений

| Номер | Наименование помещения                                          | Площадь |  |
|-------|-----------------------------------------------------------------|---------|--|
| 201   | Лестничная клетка                                               | 17.79   |  |
| 202   | Коридор                                                         | 29.91   |  |
| 203   | Кабинет                                                         | 20.23   |  |
| 204   | Кабинет                                                         | 8.71    |  |
| 205   | С/У с тамбуром                                                  | 3.69    |  |
| 206   | С/У с тамбуром                                                  | 3.69    |  |
| 207   | Кабинет                                                         | 50.31   |  |
| 208   | Техническое помещение                                           | 6.91    |  |
| 209   | Раздевалка мужская                                              | 66.35   |  |
| 210   | Техническое помещение                                           | 7.07    |  |
| 211   | Помещение рукомоёйников                                         | 7.68    |  |
| 212   | Техническое помещение<br>(Построчная с местом для сушки одежды) | 2.55    |  |
| 213   | С/У с тамбуром                                                  | 2.94    |  |
| 214   | Тамбур душевой                                                  | 5.76    |  |
| 215   | Душевая                                                         | 25.11   |  |
| 216   | Раздевалка мужская                                              | 100.98  |  |
| 217   | Тамбур душевой                                                  | 5.76    |  |
| 218   | Коридор                                                         | 7.49    |  |
| 219   | Кабинет                                                         | 9.92    |  |
| 220   | Лестничная клетка                                               | 17.79   |  |
|       | Всего                                                           | 400.61  |  |

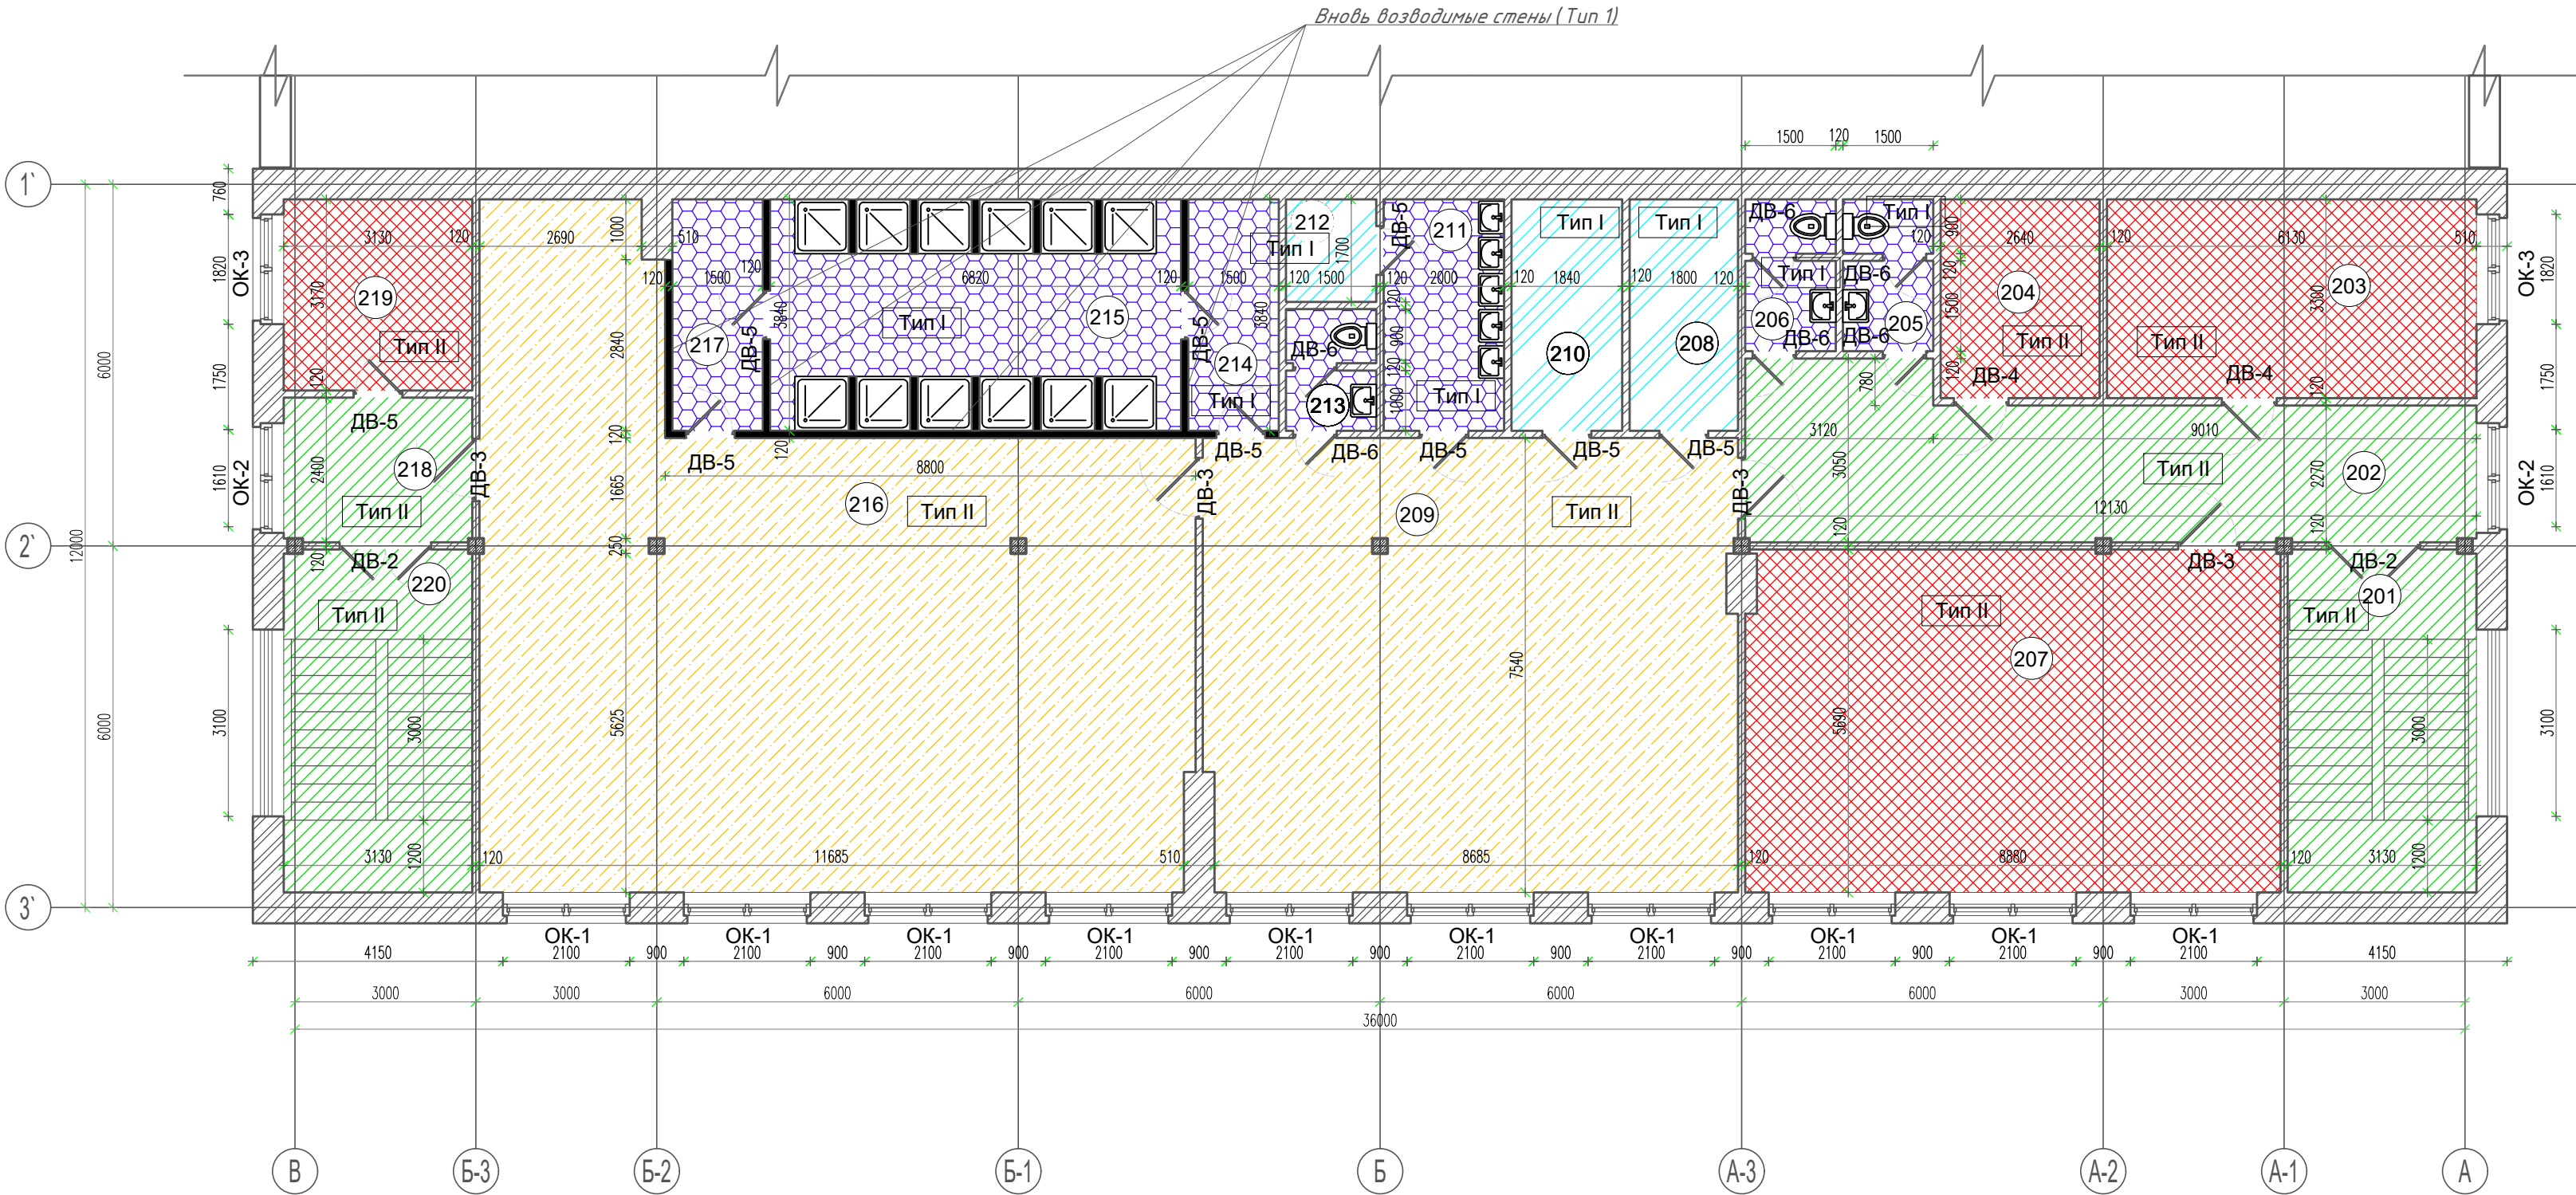


Зонирование

- Зона кабинетов и офисных помещений
- Зона коридоров и лестниц
- Зона раздевалок
- Зона помещений с мокрыми процессами
- Зона вспомогательных помещений
- Тип II Тип покрытия пола

|          |      |      |        |         |      |                                                                                      |  |                      |      |        |
|----------|------|------|--------|---------|------|--------------------------------------------------------------------------------------|--|----------------------|------|--------|
|          |      |      |        |         |      | 03-2022/4-AP                                                                         |  |                      |      |        |
|          |      |      |        |         |      | Капитальный ремонт инженерных систем здания и бытовых помещений<br>ЦРМО РМО отд. №2. |  |                      |      |        |
| Изм.     | Кол. | Лист | № док. | Подпись | Дата | Ремонт бытового корпуса                                                              |  | Стадия               | Лист | Листов |
| ГАП      |      |      |        |         |      |                                                                                      |  |                      |      |        |
| Н.контр. |      |      |        |         |      | План 2 этажа                                                                         |  | 000 "Альянс Энерджи" |      |        |
|          |      |      |        |         |      |                                                                                      |  |                      |      |        |
|          |      |      |        |         |      |                                                                                      |  |                      |      |        |

Экспликация помещений

| Номер | Наименование помещения  | Площадь |  |
|-------|-------------------------|---------|--|
| 301   | Лестничная клетка       | 17.79   |  |
| 302   | Коридор                 | 29.91   |  |
| 303   | Кабинет                 | 20.23   |  |
| 304   | Кабинет                 | 8.71    |  |
| 305   | С/У с тамбуром          | 3.69    |  |
| 306   | С/У с тамбуром          | 3.69    |  |
| 307   | Кабинет                 | 16.38   |  |
| 307а  | Кабинет                 | 16.38   |  |
| 307б  | Кабинет                 | 32.93   |  |
| 308   | Техническое помещение   | 6.91    |  |
| 309   | Раздевалка мужская      | 42.84   |  |
| 310   | Техническое помещение   | 7.07    |  |
| 311   | Помещение рукомольников | 7.68    |  |
| 312   | Техническое помещение   | 2.55    |  |
| 313   | С/У с тамбуром          | 2.94    |  |
| 314   | Предбанник душевой      | 5.76    |  |
| 315   | Душевая                 | 25.11   |  |
| 316   | Раздевалка мужская      | 100.98  |  |
| 317   | Предбанник душевой      | 5.76    |  |
| 318   | Коридор                 | 7.49    |  |
| 319   | Кабинет                 | 9.92    |  |
| 320   | Лестничная клетка       | 17.79   |  |
|       | Всего                   | 392.48  |  |

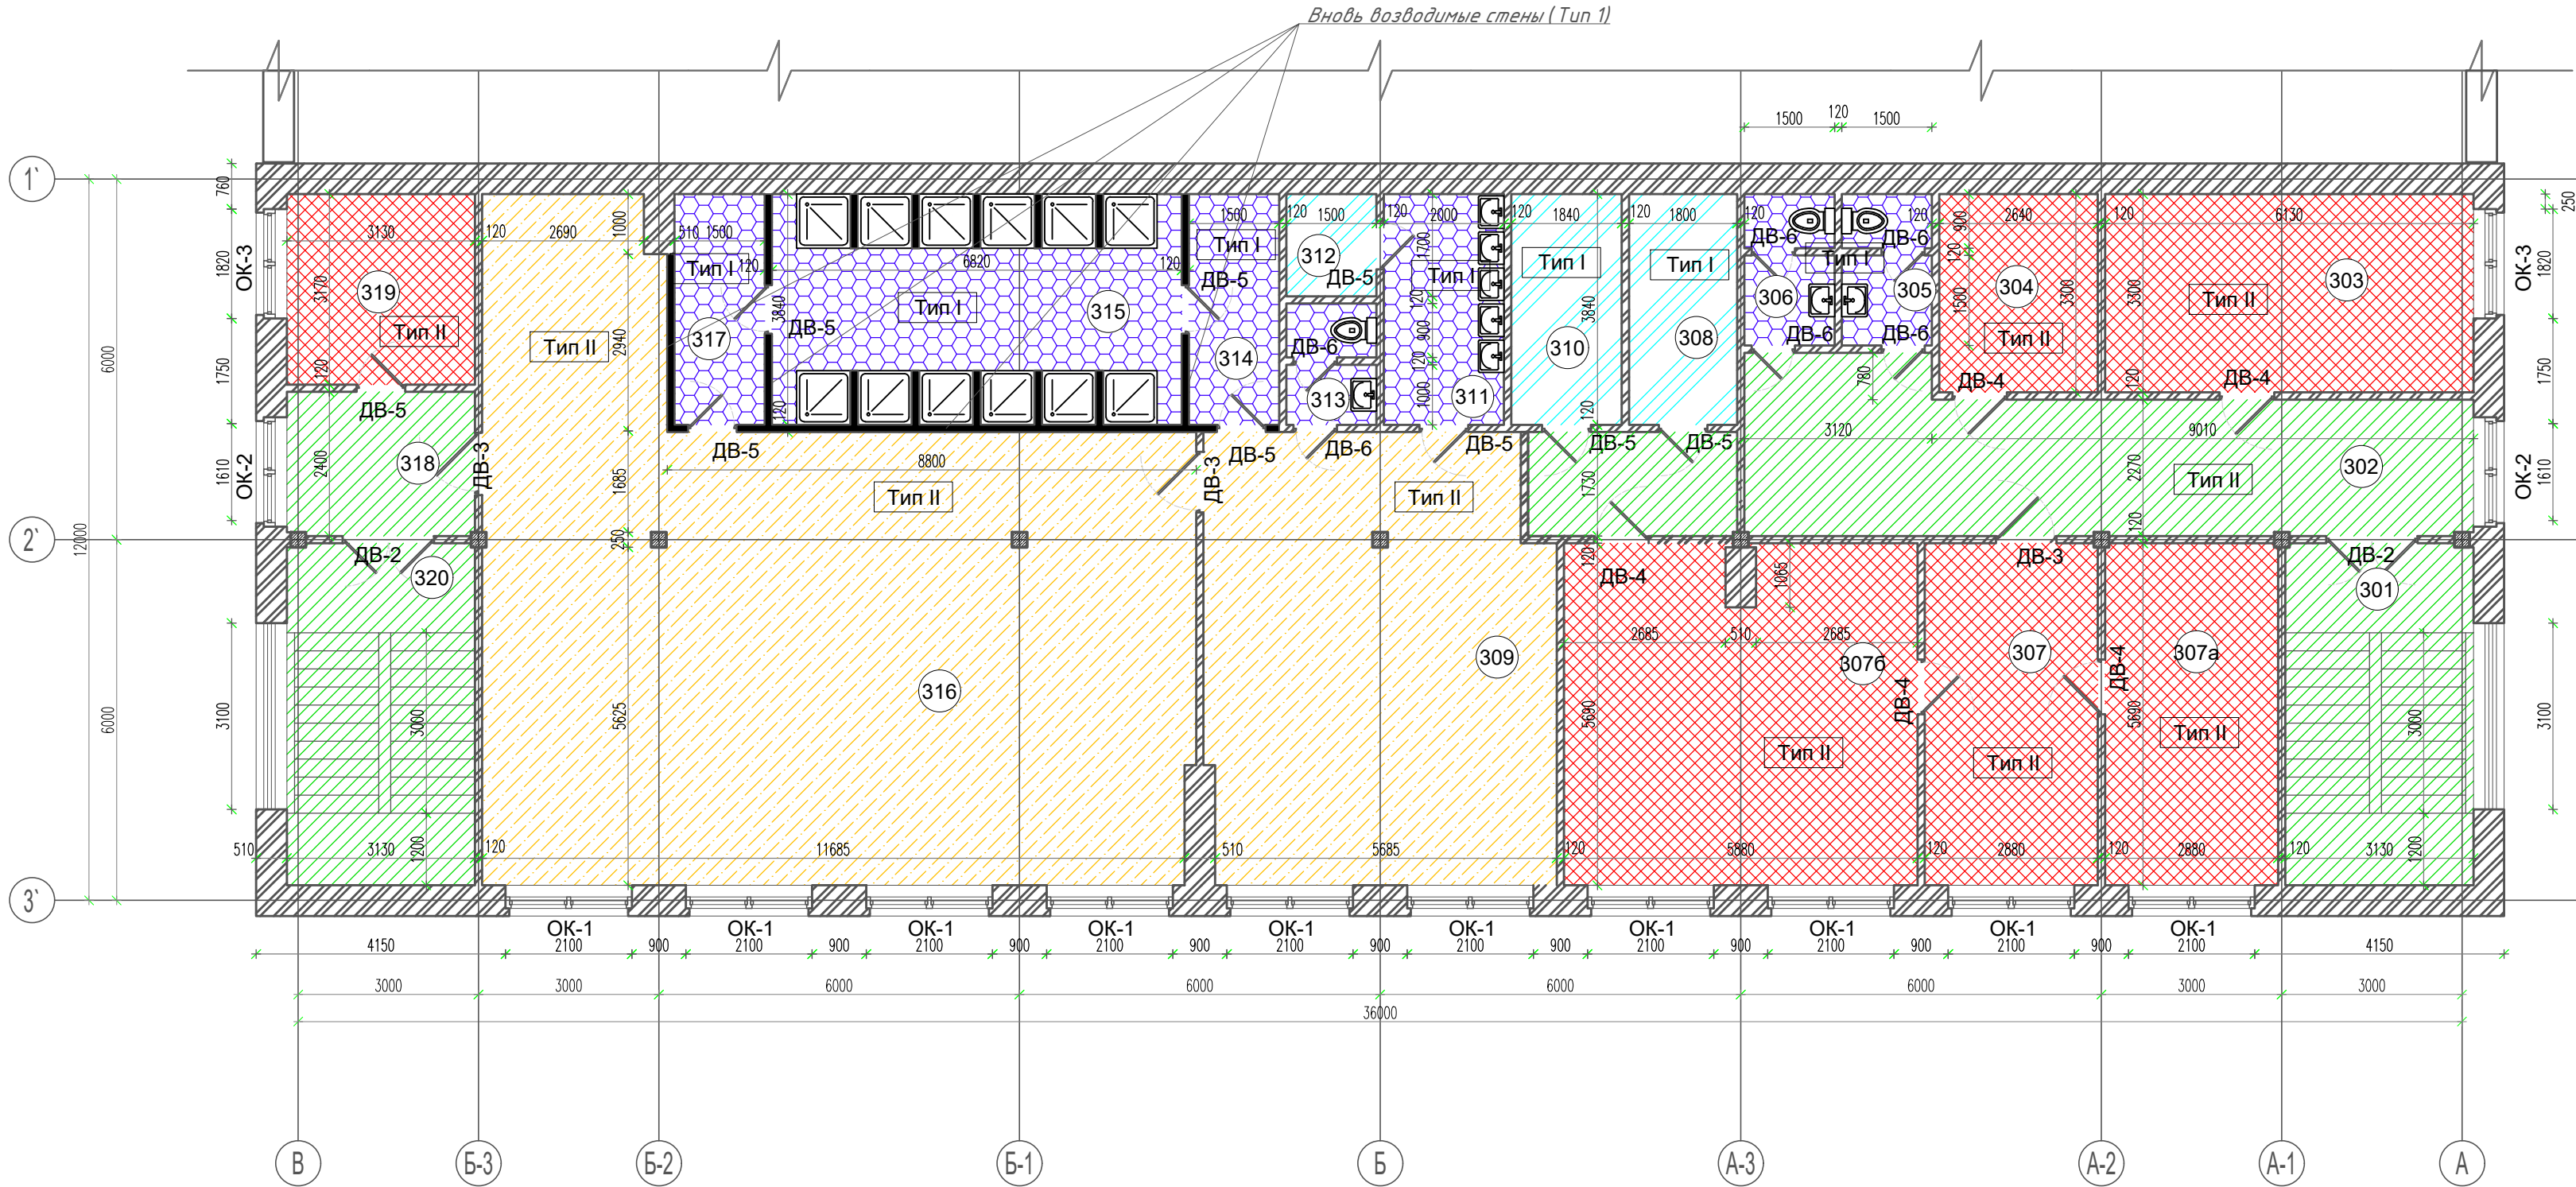

Зонирование


- Зона кабинетов и офисных помещений
- Зона коридоров и лестниц
- Зона раздевалок
- Зона помещений с мокрыми процессами
- Зона вспомогательных помещений
- Тип II Тип покрытия пола

|          |      |      |        |         |      |                                                                                   |  |                      |      |        |  |
|----------|------|------|--------|---------|------|-----------------------------------------------------------------------------------|--|----------------------|------|--------|--|
|          |      |      |        |         |      | 03-2022/4-AP                                                                      |  |                      |      |        |  |
|          |      |      |        |         |      | Капитальный ремонт инженерных систем здания и бытовых помещений ЦРМО РМО отд. №2. |  |                      |      |        |  |
| Изм.     | Кол. | Лист | № док. | Подпись | Дата | Ремонт бытового корпуса                                                           |  | Стадия               | Лист | Листов |  |
| ГАП      |      |      |        |         |      |                                                                                   |  |                      |      |        |  |
| Н.контр. |      |      |        |         |      | План 3 этажа                                                                      |  | 000 "Альянс Энерджи" |      |        |  |
|          |      |      |        |         |      |                                                                                   |  |                      |      |        |  |



Экспликация помещений

| Номер | Наименование помещения | Площадь |  |
|-------|------------------------|---------|--|
| 401   | Лестничная клетка      | 17.79   |  |
| 402   | Коридор                | 29.91   |  |
| 403   | Кабинет                | 20.23   |  |
| 404   | Кабинет                | 8.71    |  |
| 405   | С/У с тамбуром         | 3.69    |  |
| 406   | С/У с тамбуром         | 3.69    |  |
| 407   | Кабинет                | 16.38   |  |
| 407а  | Кабинет                | 16.38   |  |
| 407б  | Кабинет                | 32.93   |  |
| 408   | Техническое помещение  | 6.91    |  |
| 409   | Раздевалка мужская     | 66.35   |  |
| 410   | Техническое помещение  | 7.07    |  |
| 411   | Помещение рукомоЙников | 7.68    |  |
| 412   | Техническое помещение  | 2.55    |  |
| 413   | С/У с тамбуром         | 2.94    |  |
| 414   | Предбанник душевой     | 5.76    |  |
| 415   | Душевая                | 25.11   |  |
| 416   | Раздевалка мужская     | 100.98  |  |
| 417   | Предбанник душевой     | 5.76    |  |
| 418   | Коридор                | 7.49    |  |
| 419   | Кабинет                | 9.92    |  |
| 420   | Лестничная клетка      | 17.79   |  |
|       | Всего                  | 416.00  |  |



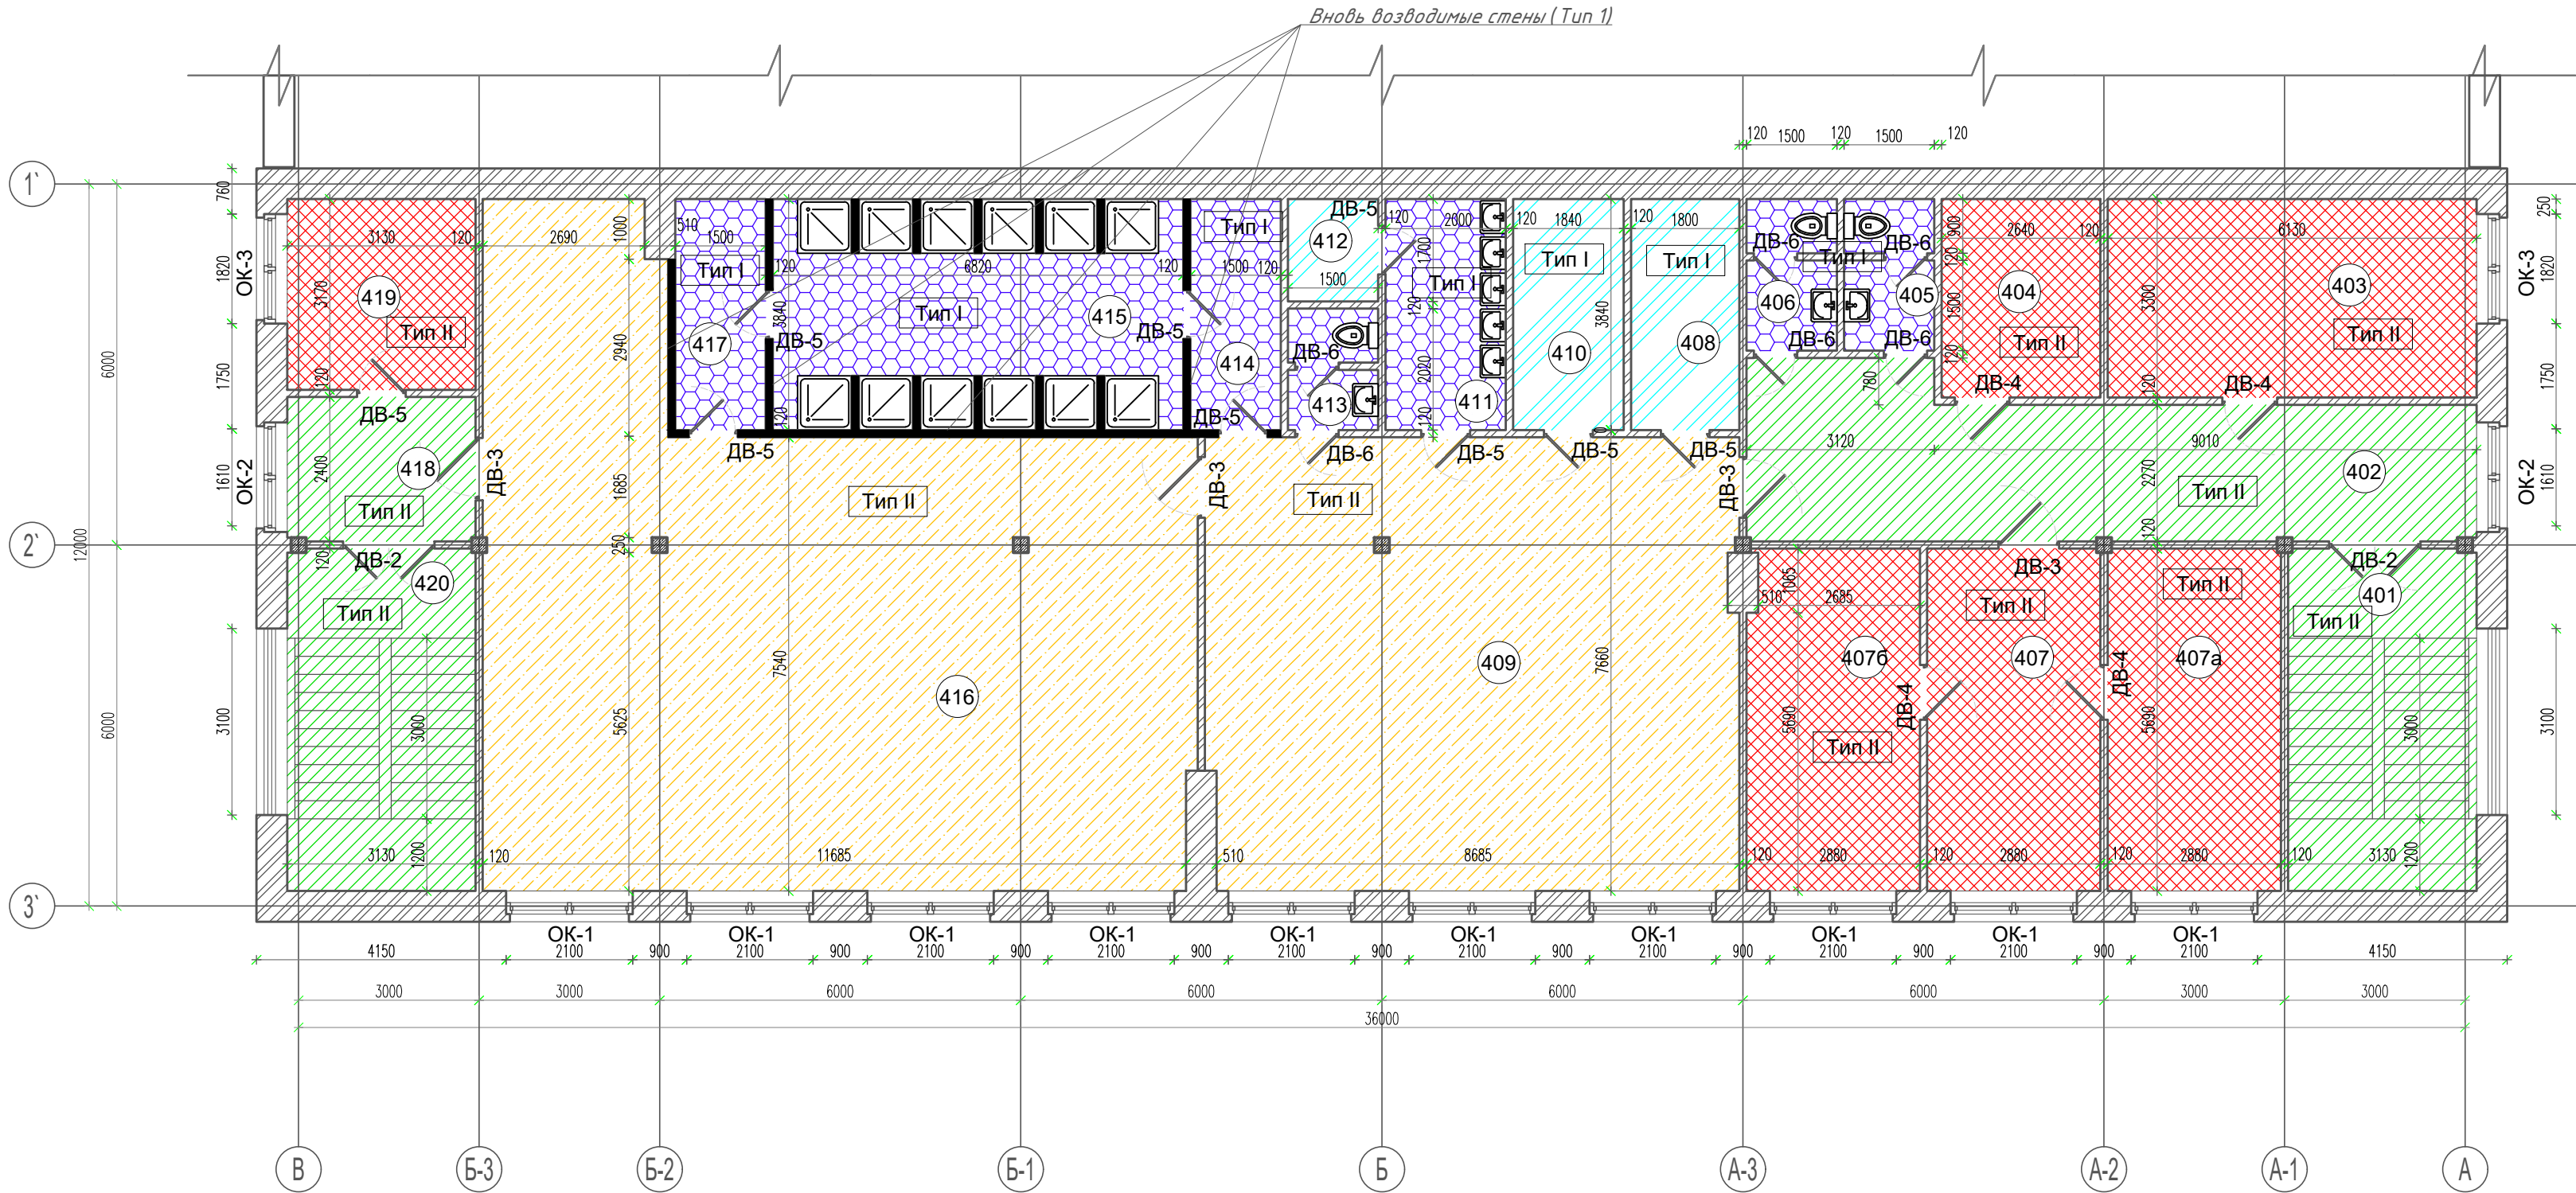


Зонирование

- Зона кабинетов и офисных помещений
- Зона коридоров и лестниц
- Зона раздевалок
- Зона помещений с мокрыми процессами
- Зона вспомогательных помещений
- Тип II Тип покрытия пола

|          |      |      |        |         |      |                                                                                   |  |  |                      |      |        |
|----------|------|------|--------|---------|------|-----------------------------------------------------------------------------------|--|--|----------------------|------|--------|
|          |      |      |        |         |      | 03-2022/4-АР                                                                      |  |  |                      |      |        |
|          |      |      |        |         |      | Капитальный ремонт инженерных систем здания и бытовых помещений ЦРМО РМО отд. №2. |  |  |                      |      |        |
| Изм.     | Кол. | Лист | № док. | Подпись | Дата | Ремонт бытового корпуса                                                           |  |  | Стадия               | Лист | Листов |
| ГАП      |      |      |        |         |      | План 4 этажа                                                                      |  |  | 000 "Альянс Энерджи" |      |        |
| Н.контр. |      |      |        |         |      |                                                                                   |  |  |                      |      |        |
|          |      |      |        |         |      |                                                                                   |  |  |                      |      |        |
|          |      |      |        |         |      |                                                                                   |  |  |                      |      |        |

Спецификация элементов заполнения дверных и оконных проемов.

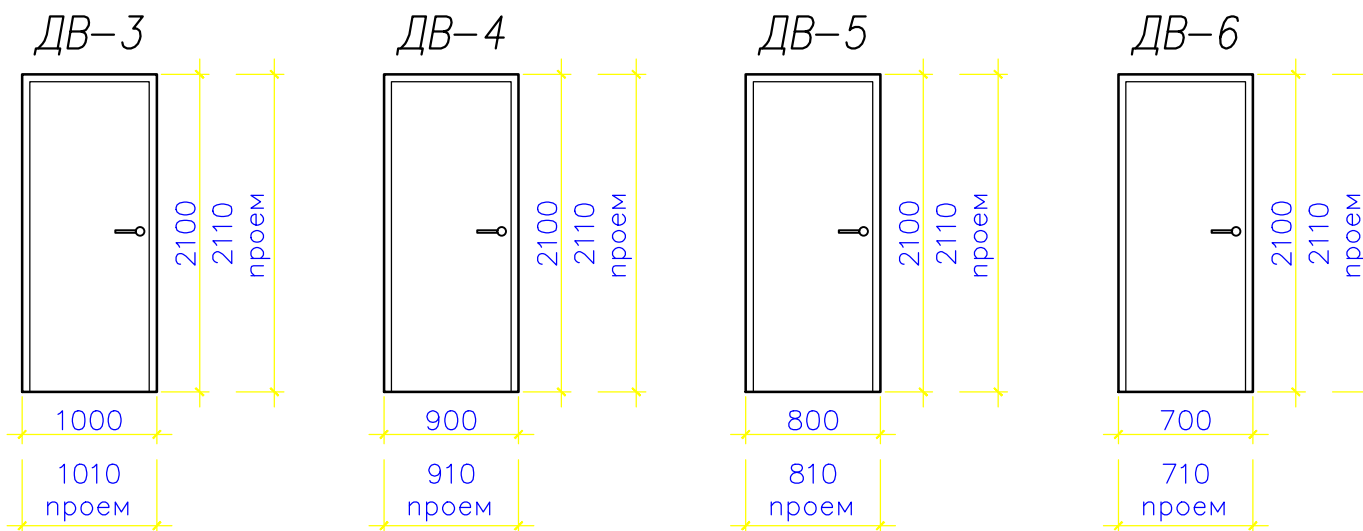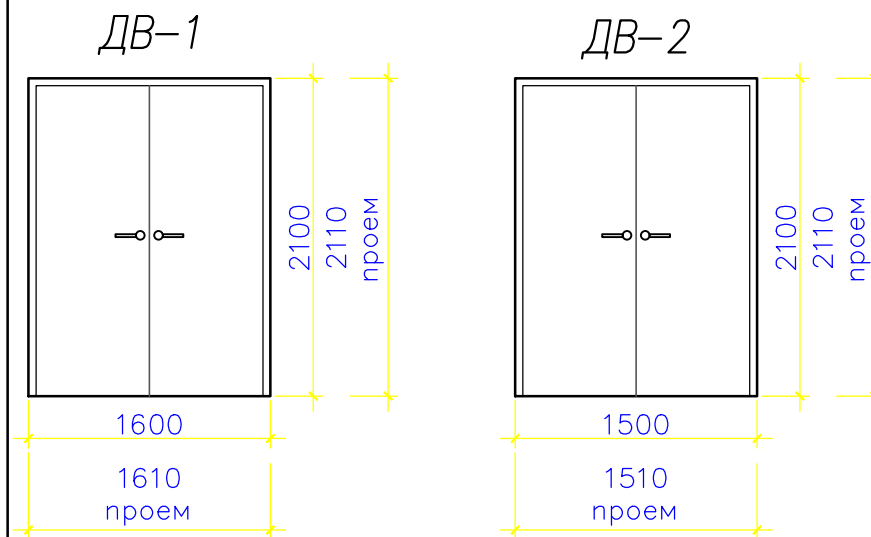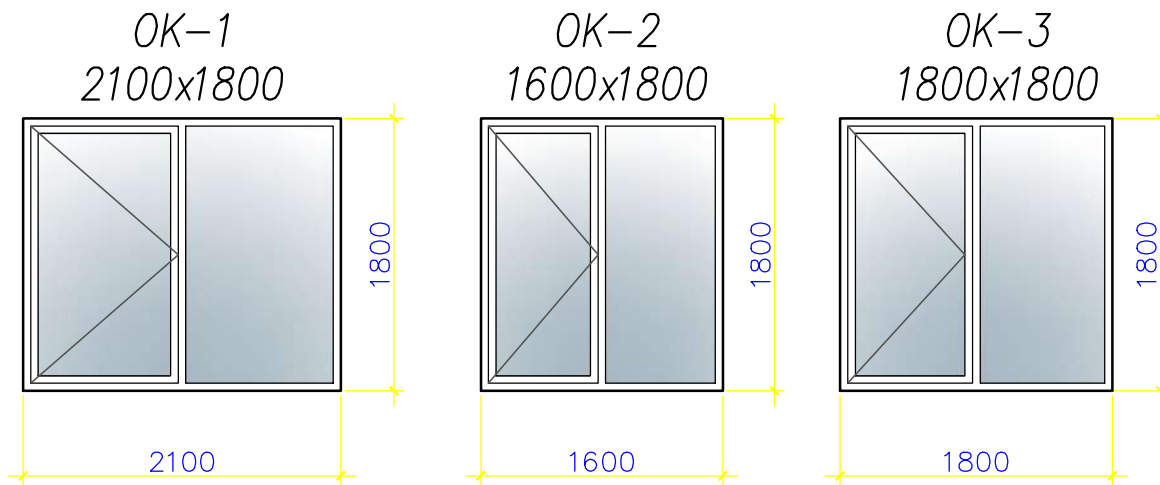


| Марка. | Обозначение.  | Наименование.                                         | Кол. | Масса<br>ед. кг. | Примечани<br>е |
|--------|---------------|-------------------------------------------------------|------|------------------|----------------|
|        |               | Окна                                                  |      |                  |                |
| ОК-1   | ГОСТ 30674-99 | Окно с двойным стеклопакетом ПВХ<br>2100х1800         | 40   |                  |                |
| ОК-2   | ГОСТ 30674-99 | Окно с двойным стеклопакетом ПВХ<br>1600х1800         | 6    |                  |                |
| ОК-3   | ГОСТ 30674-99 | Окно с двойным стеклопакетом ПВХ<br>1800х1800         | 8    |                  |                |
| ОК-В   |               | Конструкция их светопропускающих<br>блоков 3100х11720 | 2    |                  | Сущ.           |
|        |               | Двери                                                 |      |                  |                |
|        |               | Наружные                                              |      |                  |                |
| ДВ-1   |               | Дверь металлическая 2-х створчатая<br>1600х2100       | 2    |                  |                |
|        |               | Внутренние                                            |      |                  |                |
| ДВ-2   |               | Дверь 2-х створчатая<br>1500х2100                     | 8    |                  |                |
| ДВ-3   |               | Дверь 1000х2100                                       | 20   |                  |                |
| ДВ-4   |               | Дверь 900х2100                                        | 16   |                  |                |
| ДВ-5   |               | Дверь 800х2100                                        | 36   |                  |                |
| ДВ-6   |               | Дверь 700х2100                                        | 20   |                  |                |

|          |      |      |        |         |      |                                                                                      |                      |      |        |
|----------|------|------|--------|---------|------|--------------------------------------------------------------------------------------|----------------------|------|--------|
|          |      |      |        |         |      | 03-2022/4-AP                                                                         |                      |      |        |
|          |      |      |        |         |      | Капитальный ремонт инженерных систем здания и бытовых помещений<br>ЦРМО РМО отд. №2. |                      |      |        |
| Изм.     | Кол. | Лист | № док. | Подпись | Дата |                                                                                      |                      |      |        |
|          |      |      |        |         |      | Ремонт бытового корпуса                                                              | Стадия               | Лист | Листов |
| ГАП      |      |      |        |         |      |                                                                                      |                      |      |        |
| Н.контр. |      |      |        |         |      |                                                                                      |                      |      |        |
|          |      |      |        |         |      | Элементы заполнения дверных и оконных проемов                                        | ООО "Альянс Энерджи" |      |        |
|          |      |      |        |         |      |                                                                                      |                      |      |        |
|          |      |      |        |         |      |                                                                                      |                      |      |        |

Экспликация помещений




| Номер | Наименование помещения                                       | Площадь |  |
|-------|--------------------------------------------------------------|---------|--|
| 101   | Тамбур                                                       | 9.73    |  |
| 102   | Лестничная клетка                                            | 17.61   |  |
| 103   | Коридор                                                      | 26.69   |  |
| 104   | Помещение                                                    | 8.29    |  |
| 105   | Коридор                                                      | 5.77    |  |
| 106   | Помещение                                                    | 5.46    |  |
| 107   | Помещение                                                    | 7.51    |  |
| 108   | Помещение приема пищи                                        | 51.52   |  |
| 109   | Раздевалка женская                                           | 73.91   |  |
| 110   | Техническое помещение                                        | 6.96    |  |
| 111   | Помещение рукомольников                                      | 7.56    |  |
| 112   | Техническое помещение (Построчная с местом для сушки одежды) | 2.55    |  |
| 113   | Тамбур С/У                                                   | 1.50    |  |
| 114   | С/У                                                          | 1.26    |  |
| 115   | Душевые с тамбуром                                           | 20.77   |  |
| 116   | Тренажерный зал                                              | 58.50   |  |
| 117   | Коридор                                                      | 13.90   |  |
| 118   | Душевые с тамбуром                                           | 15.50   |  |
| 119   | Сауна                                                        | 11.14   |  |
| 120   | Комната отдыха                                               | 16.38   |  |
| 121   | Тамбур                                                       | 6.13    |  |
| 122   | Коридор                                                      | 3.37    |  |
| 123   | Тех. помещение                                               | 1.08    |  |
| 124   | Лестничная клетка                                            | 17.61   |  |
| Всего |                                                              | 390.69  |  |

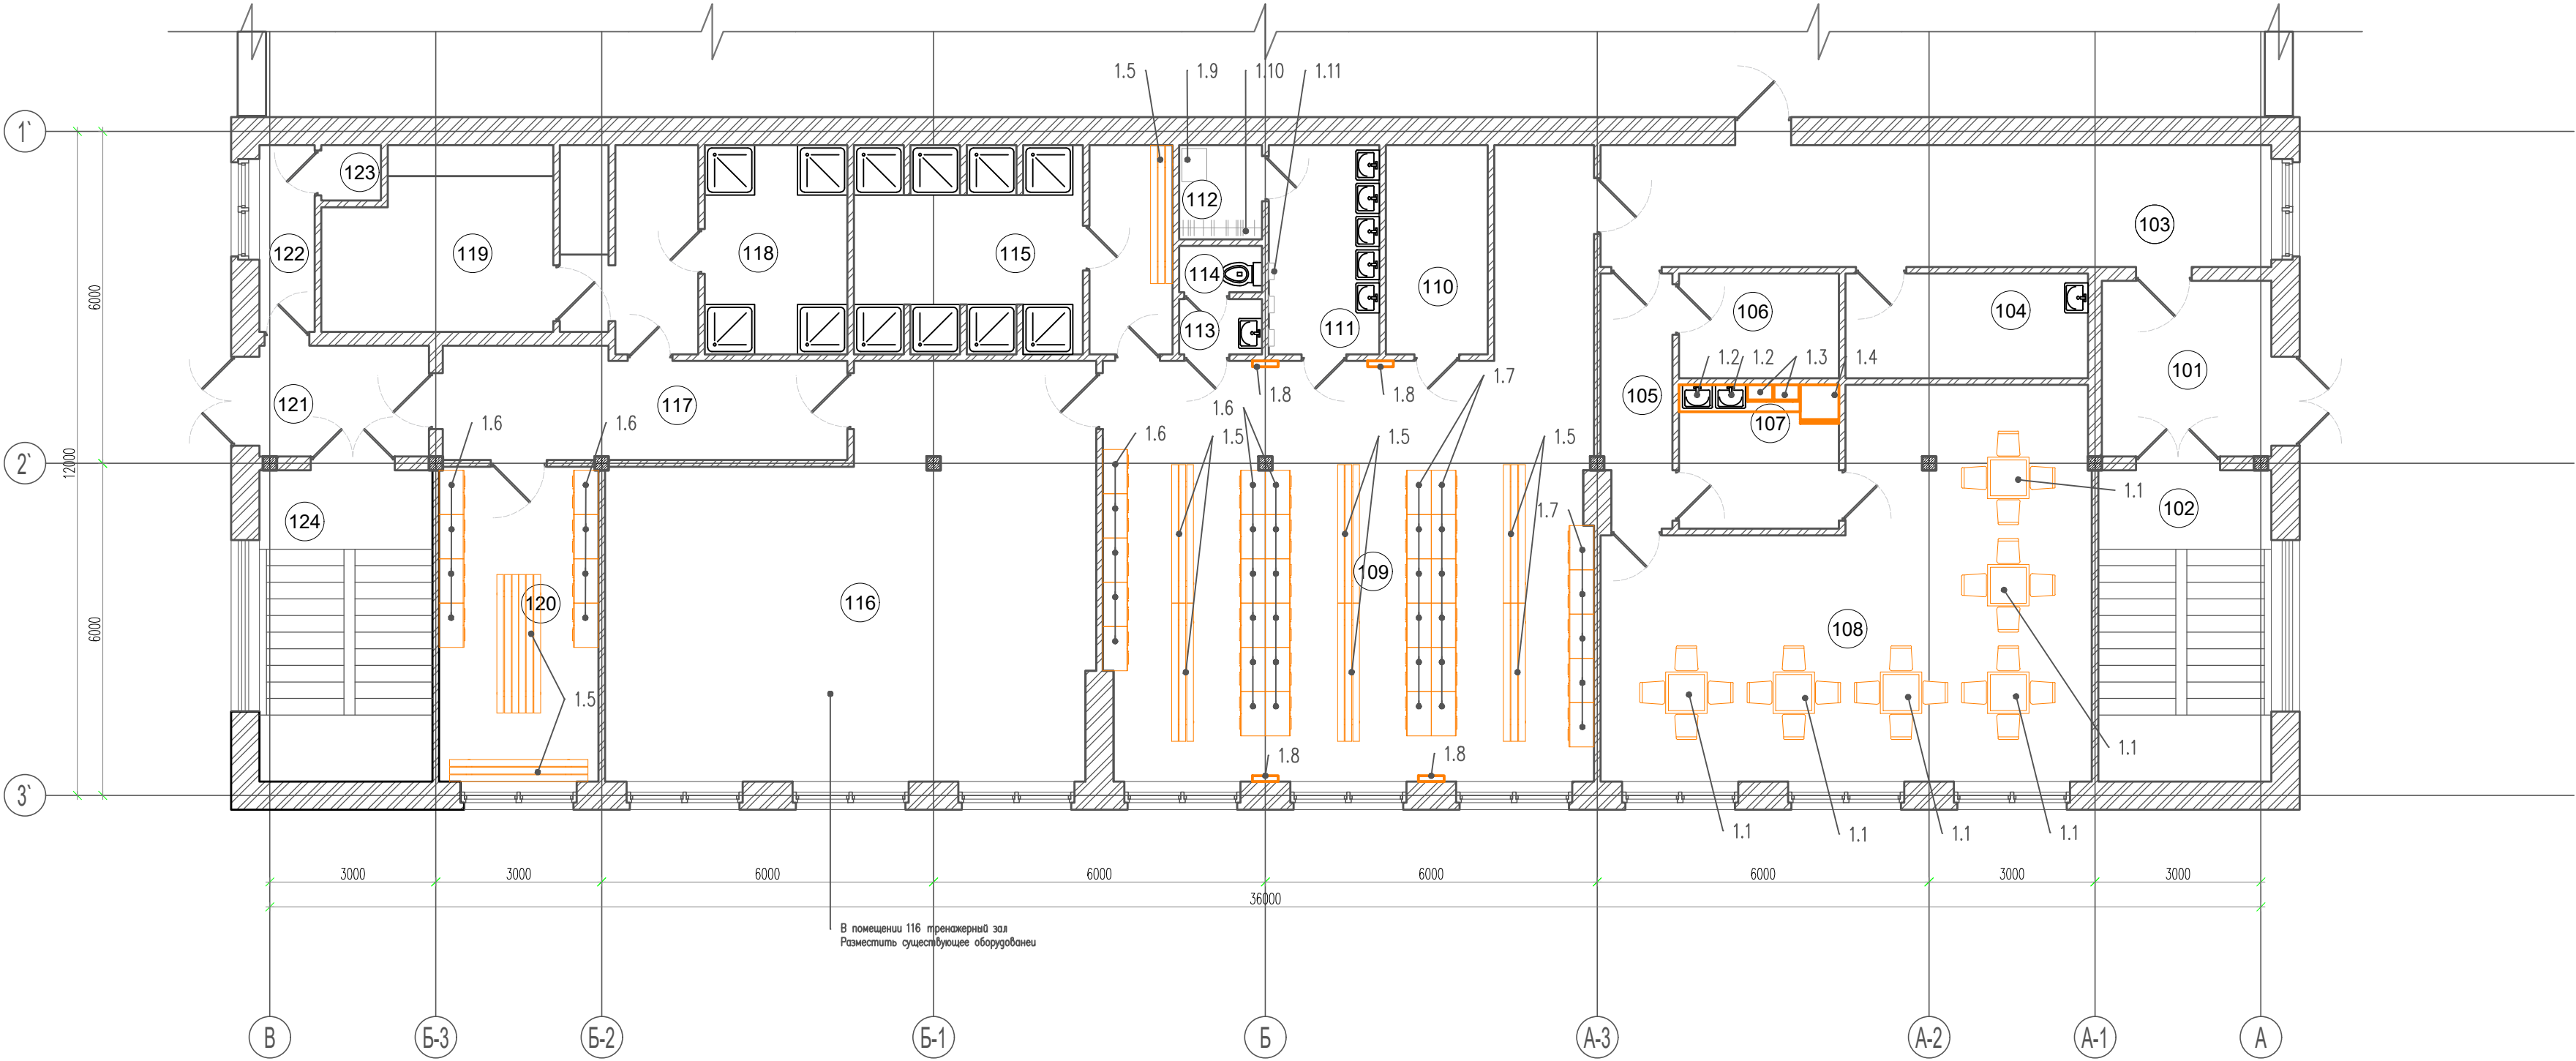






|          |      |      |        |         |      |                                                                                   |                      |      |        |
|----------|------|------|--------|---------|------|-----------------------------------------------------------------------------------|----------------------|------|--------|
|          |      |      |        |         |      | 03-2022/4-AP                                                                      |                      |      |        |
|          |      |      |        |         |      | Капитальный ремонт инженерных систем здания и бытовых помещений ЦРМО РМО отд. №2. |                      |      |        |
| Изм.     | Кол. | Лист | № док. | Подпись | Дата | Ремонт бытового корпуса                                                           | Стадия               | Лист | Листов |
| ГАП      |      |      |        |         |      |                                                                                   |                      |      |        |
| Н.контр. |      |      |        |         |      | План 1 этажа<br>Оборудование                                                      | 000 "Альянс Энерджи" |      |        |
|          |      |      |        |         |      |                                                                                   |                      |      |        |

Развертки по стенам





Помещения 109

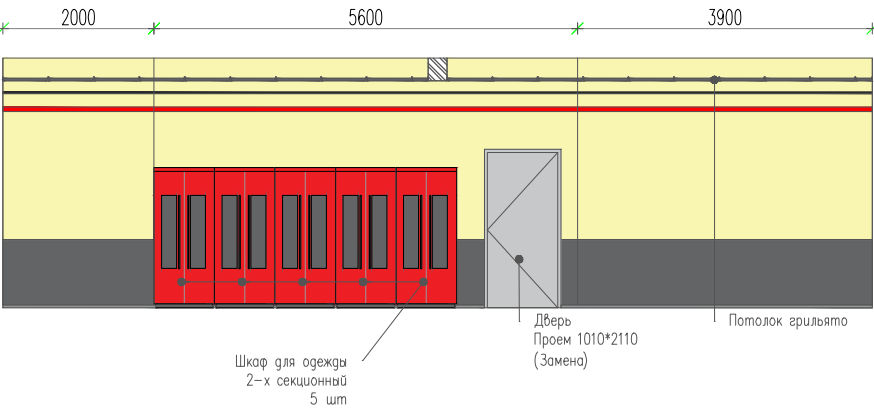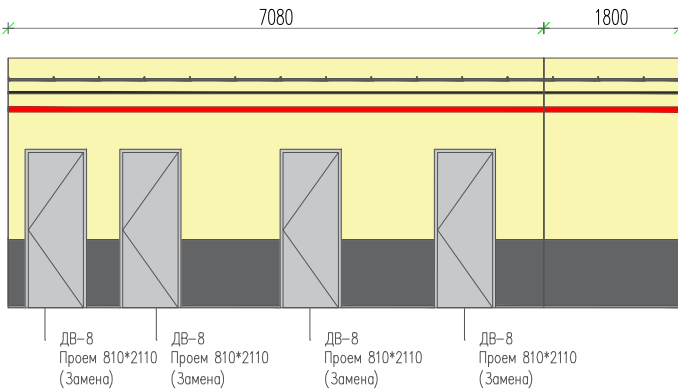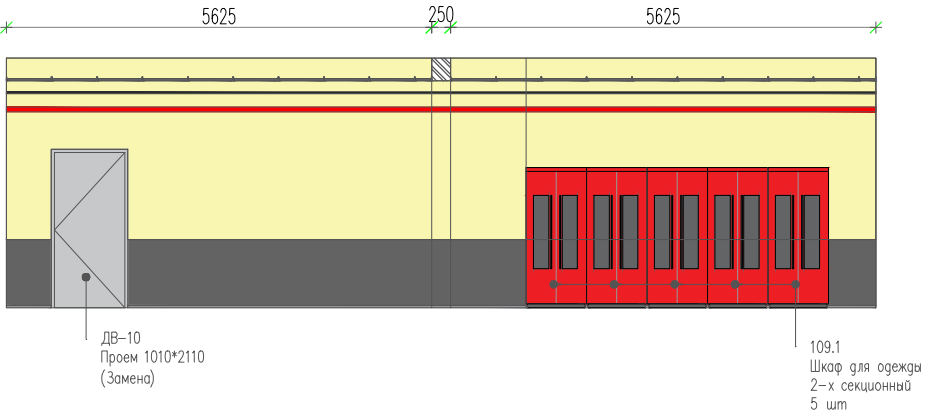


Помещения 111

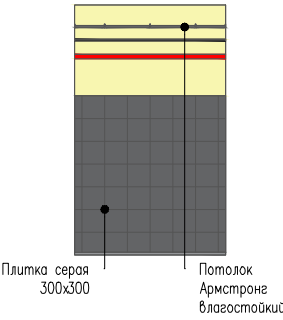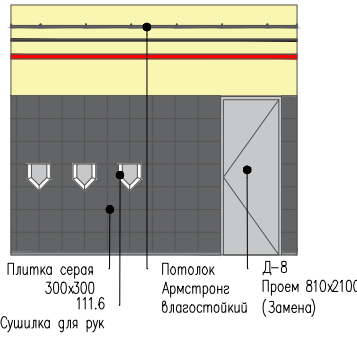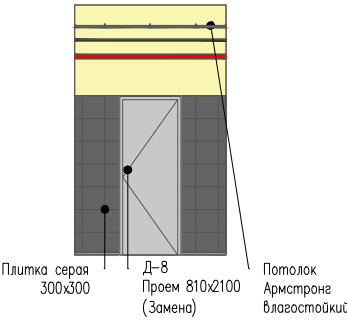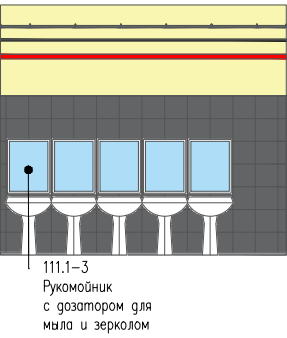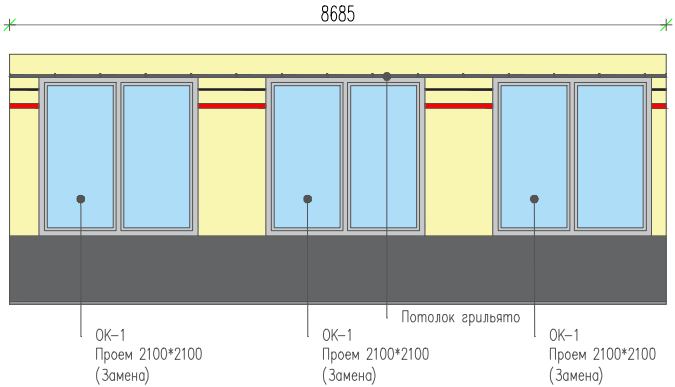

Помещения 108

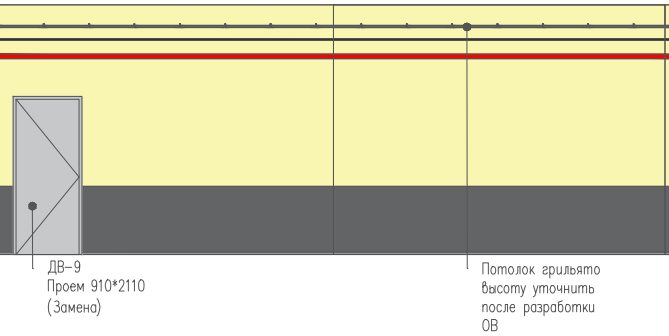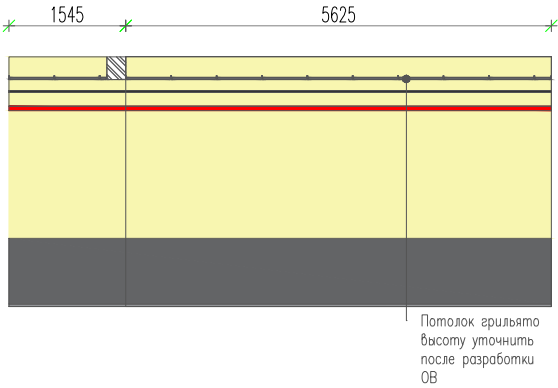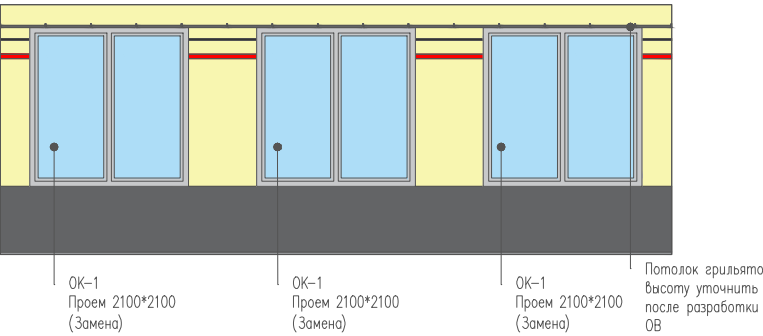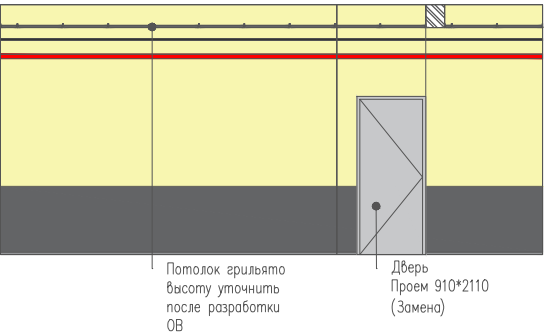

Помещения 112


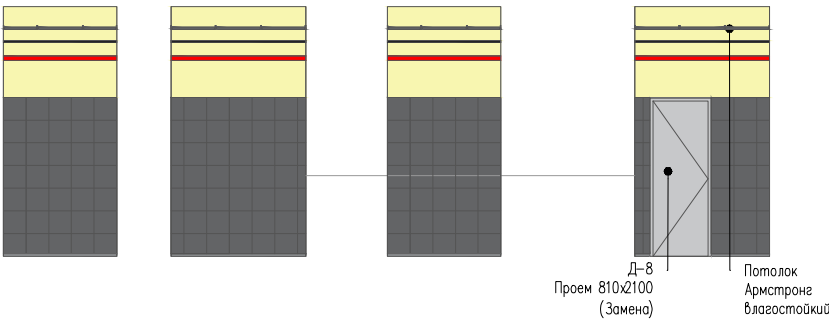


|          |      |      |        |         |      |                                                                                      |                      |        |
|----------|------|------|--------|---------|------|--------------------------------------------------------------------------------------|----------------------|--------|
|          |      |      |        |         |      | 03-2022/4-AP                                                                         |                      |        |
|          |      |      |        |         |      | Капитальный ремонт инженерных систем здания и бытовых помещений<br>ЦРМО РМО отд. №2. |                      |        |
| Изм.     | Кол. | Лист | № док. | Подпись | Дата | Ремонт бытового корпуса                                                              | Стадия               | Лист   |
| ГАП      |      |      |        |         |      |                                                                                      |                      | Листов |
| Н.контр. |      |      |        |         |      | Развертки помещений                                                                  | ООО "Альянс Энерджи" |        |
|          |      |      |        |         |      |                                                                                      |                      |        |




План помещения 111 и 112


Развертки по стенам помещение 111

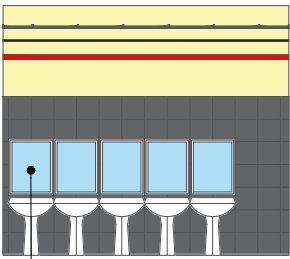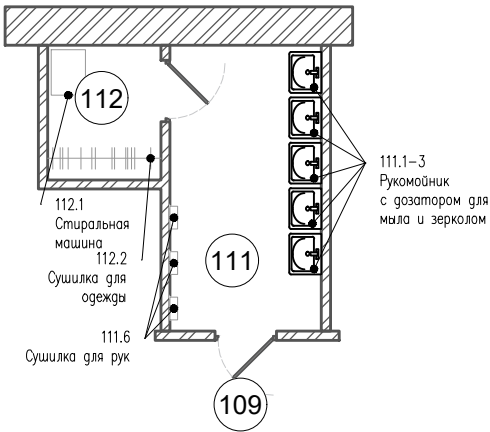


111.1-3  
Рукомойник  
с дозатором для  
мыла и зеркалом

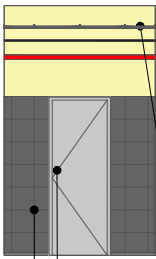

Плитка серая  
300x300  
Д-8  
Проем 810x2100  
(Замена)  
Потолок  
Армстронг  
водостойкий



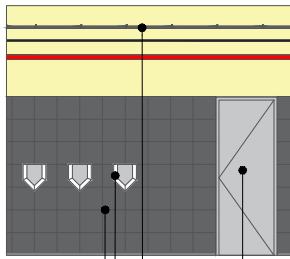


Плитка серая  
300x300  
111.6  
Сушилка для рук  
Потолок  
Армстронг  
водостойкий  
Д-8  
Проем 810x2100  
(Замена)

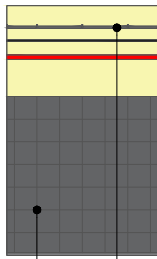

Плитка серая  
300x300  
Потолок  
Армстронг  
водостойкий

Развертки по стенам помещение 112

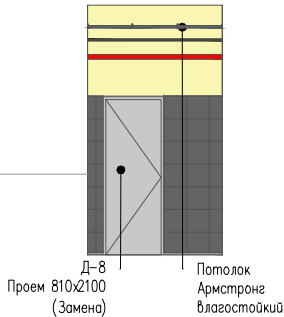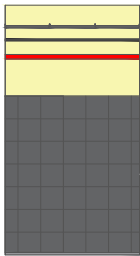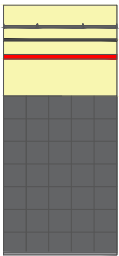

Д-8  
Проем 810x2100  
(Замена)  
Потолок  
Армстронг  
водостойкий

По помещению 111

1. Площадь пола – 7,50 кв.м.
2. Площадь подвесного потолка армстронг водостойкий – 7,5 кв.м.
3. Площадь стен без учета откосов от 0,00 до +2,10 (плитка 300x300) – 20,8 кв.м.
3. Площадь стен без учета откосов от +2,10 до +3,00 (окраска) – 10,4 кв.м.
4. Замена дверных блоков – 2 шт (3,4 кв.м.)
5. Периметр помещения 11,50 м.

По помещению 112

1. Площадь пола – 6,95 кв.м.
2. Площадь подвесного потолка армстронг водостойкий – 6,95 кв.м.
3. Площадь стен без учета откосов от 0,00 до +2,10 (плитка 300x300) – 12,0 кв.м.
3. Площадь стен без учета откосов от +2,10 до +3,00 (окраска) – 5,9 кв.м.
4. Замена дверных блоков – 1 шт (1,7 кв.м.)
5. Периметр помещения 6,50 м.

Ведомость оборудования

| Поз.  | Наименование и техническая характеристика | Ед. изме- рения | Кол. | Примечания          |
|-------|-------------------------------------------|-----------------|------|---------------------|
| 111.1 | Рукомойник с краном                       | шт.             | 5    |                     |
| 111.2 | Зеркало                                   | шт.             | 5    |                     |
| 111.3 | Дозатор для мыла                          | шт.             | 5    |                     |
| 111.4 | Диспенсер для бумажных полотенец          | шт.             | 2    | установить по месту |
| 111.5 | Ведро мусорное                            | шт.             | 2    | установить по месту |
| 111.6 | Сушилки для рук                           | шт.             | 3    |                     |
| 112.1 | Стиральная машина                         | шт.             | 1    |                     |
| 112.2 | Сушилка для одежды                        | шт.             | 1    |                     |

Примечание:

1. По аналогии с данным помещением выполнить помещения рукомойников и сан узлов на всех этажах.
2. Во избежании удвоения объемов – объемы работ брать из сводной ведомости. объемы по помещению на данном листе даны для ознакомления.

|          |      |      |        |         |      |                                                                                      |                      |      |        |
|----------|------|------|--------|---------|------|--------------------------------------------------------------------------------------|----------------------|------|--------|
|          |      |      |        |         |      | 03-2022/4-AP                                                                         |                      |      |        |
|          |      |      |        |         |      | Капитальный ремонт инженерных систем здания и бытовых помещений<br>ЦРМО РМО отд. №2. |                      |      |        |
| Изм.     | Кол. | Лист | № док. | Подпись | Дата |                                                                                      |                      |      |        |
|          |      |      |        |         |      | Ремонт бытового корпуса                                                              | Стадия               | Лист | Листов |
| ГАП      |      |      |        |         |      |                                                                                      |                      |      |        |
| Н.контр. |      |      |        |         |      |                                                                                      |                      |      |        |
|          |      |      |        |         |      | Помещение 108                                                                        | ООО "Альянс Энерджи" |      |        |
|          |      |      |        |         |      |                                                                                      |                      |      |        |
|          |      |      |        |         |      |                                                                                      |                      |      |        |

|                                   |
|-----------------------------------|
| Ведомость оборудования на 1 этаже |
|-----------------------------------|

| Поз. | Наименование и техническая характеристика       | Ед. изме-<br>рения | Кол. | Примечания |
|------|-------------------------------------------------|--------------------|------|------------|
| 1.1  | Стол обеденный 750х750<br>4 стула ИЗО           | шт.                | 6    |            |
| 1.2  | Стол с врезной мойкой (2 шт).                   | шт.                | 24   |            |
| 1,3  | Микроволновка                                   | шт.                | 2    |            |
| 1,4  | Холодильник                                     | шт.                | 1    |            |
| 1,5  | Скамья гардеробная                              | шт.                | 9    |            |
| 1.6  | Шкаф для одежды 2-х секционный                  | шт.                | 25   |            |
| 1.7  | Шкаф для одежды 2-х секционный с функцией сушки | шт.                | 17   |            |
| 1.8  | Зеркало<br>Фен                                  | шт.                | 4    |            |
| 1.9  | Стиральная машина                               | шт.                | 1    |            |
| 1.10 | Вешалка для сушки одежды                        | шт.                | 1    |            |
|      | Помещение 111                                   |                    |      |            |
| 1.11 | Сушилка для рук                                 | шт.                | 3    |            |
|      | Дозатор для мыла                                | шт.                | 5    | Прим.1     |
|      | Диспенсер для бумажных полотенец                | шт.                | 2    | Прим.1     |
|      | Мусорное ведро (большое)                        | шт.                | 2    | Прим.1     |
|      | Зеркала на стену                                | шт.                | 5    | Прим.1     |
|      | Рукомойники                                     | шт.                | 5    |            |
|      | Помещение 113 и 114                             |                    |      |            |
|      | Унитаз                                          | шт.                | 1    | Прим.1     |
|      | Диспенсер для туалетной бумаги                  | шт.                | 1    | Прим.1     |
|      | Дозатор для мыла                                | шт.                | 1    | Прим.1     |
|      | Ведро для мусора                                | шт.                | 2    | Прим.1     |
|      | Диспенсер для бумажных полотенец                | шт.                | 1    | Прим.1     |
|      | Сушилка для рук                                 | шт.                | 1    | Прим.1     |
|      | Зеркало на стену                                |                    |      |            |

| Поз. | Наименование и техническая характеристика           | Ед. изме- рения | Кол.    | Примечания |
|------|-----------------------------------------------------|-----------------|---------|------------|
|      | Помещение 115 и 118                                 |                 |         |            |
|      | Вешалки для одежды                                  | шт.             | 10х2=20 | Прим.1     |
|      | Душевые поддоны                                     | шт.             | 12      | Прим.1     |
|      | Полки навесные на стену для душа                    | шт.             | 12      | Прим.1     |
|      | Сушилки для полотенец электрические (в предбаннике) | шт.             | 12      | Прим.1     |
|      | Коврики резиновые для душевых помещений 1х2м        | шт.             | 12      | Прим.1     |
|      |                                                     |                 |         |            |
|      |                                                     |                 |         |            |
Примечания:


1. Установить по месту.
2. Остальные этажи сделать по аналогии с 1 этажом.
3. Офисные помещения (кабинеты) проектируются из расчета 6-7 кв.м. на одно рабочее место. Для более точной проработки прошу указать количество рабочих мест каждого кабинета или его функциональное назначение которое требуется от данного помещения.

|          |      |      |        |         |      |                                                                                      |                      |      |        |
|----------|------|------|--------|---------|------|--------------------------------------------------------------------------------------|----------------------|------|--------|
|          |      |      |        |         |      | 03-2022/4-AP                                                                         |                      |      |        |
|          |      |      |        |         |      | Капитальный ремонт инженерных систем здания и бытовых помещений<br>ЦРМО РМО отд. №2. |                      |      |        |
| Изм.     | Кол. | Лист | № док. | Подпись | Дата |                                                                                      |                      |      |        |
|          |      |      |        |         |      | Ремонт бытового корпуса                                                              | Стадия               | Лист | Листов |
| ГАП      |      |      |        |         |      |                                                                                      |                      |      |        |
| Н.контр. |      |      |        |         |      |                                                                                      |                      |      |        |
|          |      |      |        |         |      | Ведомость оборудования на 1 этаж                                                     | ООО "Альянс Энерджи" |      |        |
|          |      |      |        |         |      |                                                                                      |                      |      |        |
|          |      |      |        |         |      |                                                                                      |                      |      |        |



## Узел А


Перегородки вновь возводимые

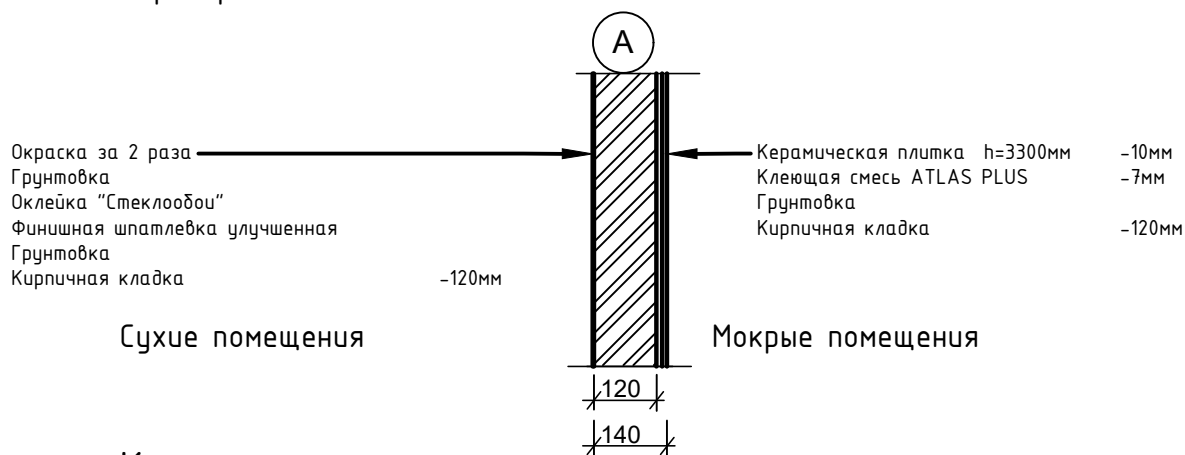

## Конструкция пола


Тип I

Пол с покрытием из плитки

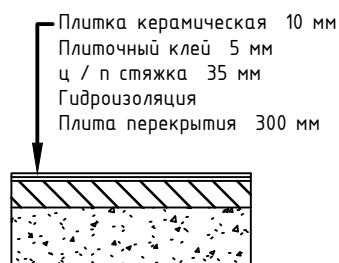

Тип II

Пол полиуретановый наливной

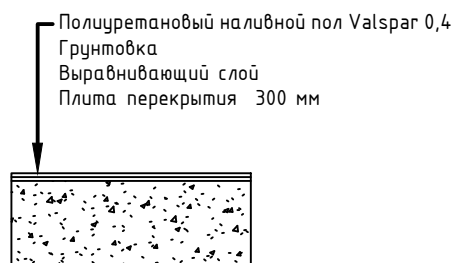

Примечание:

- Перегородки санузлов выполнить из керамического кирпича КОРПо 1НФ/100/2,0/25 ГОСТ 530-2007.на растворе М-50. Перегородки армировать сетками Ф4Вр1 (шаг50х50) через 6 рядов кладки по высоте.
- Над проемами в кирпичных перегородках положить перемычки 8ПБ13-1 (4шт.).
- Размеры на плане даны без учёта наружной облицовки.
- Возводимые стены и типы полов замаркированы на листах планов этажей.
- Объем возводимых конструкций:
  - 1 этаж - 92,4 куб.м.
  - 2 этаж - 97,4 куб.м.
  - 3 этаж - 97,4 куб.м.
  - 4 этаж - 97,4 куб.м.

Итого: 384,6 куб.м.

|          |      |      |        |         |      |                                                                                      |                      |      |        |
|----------|------|------|--------|---------|------|--------------------------------------------------------------------------------------|----------------------|------|--------|
|          |      |      |        |         |      | 03-2022/4-AP                                                                         |                      |      |        |
|          |      |      |        |         |      | Капитальный ремонт инженерных систем здания и бытовых помещений<br>ЦРМО РМО отд. №2. |                      |      |        |
| Изм.     | Кол. | Лист | № док. | Подпись | Дата |                                                                                      |                      |      |        |
| ГАП      |      |      |        |         |      | Ремонт бытового корпуса                                                              | Стадия               | Лист | Листов |
| Н.контр. |      |      |        |         |      |                                                                                      |                      |      |        |
|          |      |      |        |         |      | Узел А<br>(перегородки вновь возводимые)<br>Конструкция пола                         | ООО "Альянс Энерджи" |      |        |
|          |      |      |        |         |      |                                                                                      |                      |      |        |
|          |      |      |        |         |      |                                                                                      |                      |      |        |

| Ведомость отделки помещений<br>Площадь, м <sup>2</sup> |   |              |   |              |                                                                            |              |            |
|--------------------------------------------------------|---|--------------|---|--------------|----------------------------------------------------------------------------|--------------|------------|
| Наименование или номер помещения                       | Вид отделки элементов интерьера   |              |   |              |                                                                            |              | Примечание |
|                                                        | Потолок   | Пло-<br>щадь | Стены или перегородки   | Пло-<br>щадь | Полы                                                                       | Пло-<br>щадь |            |
| 101_ Тамбур                                            | Грунтовка запотолочного пространства.<br>Штукатурка запотолочного пространства.<br>Грунтовка запотолочного пространства.<br>Окраска запотолочного пространства – краска для стен и потолков Текс «Профи» влагостойкая база А – 2 слоя.<br>Потолок грильято 150х150 серебристый алюминий (h=50; b=10) ЦСС.<br><br>Далее Тип: Грильято 150х150 серебристый алюминий | 9,73         | Грунтовка<br>Штукатурка<br>Грунтовка<br>Краска для стен и потолков Текс «Профи» влагостойкая база А – 2 слоя.<br><br>Далее Тип: Окраска стен Текс «Профи» | 39,60        | Полиуретановый наливной пол Valspar 0,4                                    | 9,73         |            |
| 103_Коридор                                            | Грильято 150х150 серебристый алюминий   | 26,69        | Окраска стен Текс «Профи»   | 92,40        | Полиуретановый наливной пол Valspar 0,4                                    | 26,69        |            |
| 104_ Помещение                                         | Грильято 150х150 серебристый алюминий   | 8,29         | от отм 0,00 до отм.: +2.100<br>Грунтовка<br>Плиточный клей – 5 мм<br>Плитка 300х300 – 10 мм                                                               | 25,20        | Гидроизоляция<br>Плиточный клей – 5 мм<br>Плитка напольная 300х300 – 10 мм | 8,29         |            |
|                                                        |   |              | от отм 2,10 до отм.: +3.30<br>по типу Окраска стен Текс «Профи»                                                                                           | 14,40        |                                                                            |              |            |
| 105_Коридор                                            | Грильято 150х150 серебристый алюминий   | 5,77         | Окраска стен Текс «Профи»   | 34,65        | Полиуретановый наливной пол Valspar 0,4                                    | 5,77         |            |
| 106_ Помещение                                         | Грильято 150х150 серебристый алюминий   | 5,46         | от отм 0,00 до отм.: +2.100<br>Грунтовка<br>Плиточный клей – 5 мм<br>Плитка 300х300 – 10 мм                                                               | 18,90        | Гидроизоляция<br>Плиточный клей – 5 мм<br>Плитка напольная 300х300 – 10 мм | 5,46         |            |
|                                                        |   |              | от отм 2,10 до отм.: +3.30<br>по типу Окраска стен Текс «Профи»                                                                                           | 10,80        |                                                                            |              |            |
| 107_ Помещение                                         | Грильято 150х150 серебристый алюминий   | 7,51         | от отм 0,00 до отм.: +2.100<br>Грунтовка<br>Плиточный клей – 5 мм<br>Плитка 300х300 – 10 мм                                                               | 21,00        | Гидроизоляция<br>Плиточный клей – 5 мм<br>Плитка напольная 300х300 – 10 мм | 7,51         |            |
|                                                        |   |              | от отм 2,10 до отм.: +3.30<br>по типу Окраска стен Текс «Профи»                                                                                           | 12,00        |                                                                            |              |            |
| 108_ Помещение приема пищи                             | Грильято 150х150 серебристый алюминий   | 51,52        | Окраска стен Текс «Профи»   | 100,00       | Полиуретановый наливной пол Valspar 0,4                                    | 55,00        |            |
| 109_Раздевалка женская                                 | Грильято 150х150 серебристый алюминий   | 73,91        | Окраска стен Текс «Профи»   | 125,40       | Полиуретановый наливной пол Valspar 0,4                                    | 76,00        |            |

Примечание:  
1. По аналогии с данным помещением выполнить помещения рукомоёйников и сан узлов на всех этажах.  
2. Во избежании задвоения объемов – объемы работ брать из сводной ведомости. объемы по помещению на данном листе даны для ознакомления.

|                 |      |      |       |         |      |                                                                                   |                      |      |        |
|-----------------|------|------|-------|---------|------|-----------------------------------------------------------------------------------|----------------------|------|--------|
|                 |      |      |       |         |      | 03-2022/4-AP                                                                      |                      |      |        |
|                 |      |      |       |         |      | Капитальный ремонт инженерных систем здания и бытовых помещений ЦРМО РМО отд. №2. |                      |      |        |
| Изм.            | Кол. | Лист | №док. | Подпись | Дата |                                                                                   |                      |      |        |
|                 |      |      |       |         |      | Ремонт бытового корпуса                                                           | Стадия               | Лист | Листов |
| ГАП<br>Н.контр. |      |      |       |         |      |                                                                                   |                      |      |        |
|                 |      |      |       |         |      | Ведомость отделки помещений первого этажа (начало 1/3)                            | ООО “Альянс Энерджи” |      |        |
|                 |      |      |       |         |      |                                                                                   |                      |      |        |

Ведомость отделки помещений

Площадь, м²

| Наименование или номер помещения                                 | Вид отделки элементов интерьера           |         |   |                        |   |         | Примечание |
|------------------------------------------------------------------|-------------------------------------------|---------|---|------------------------|---|---------|------------|
|                                                                  | Потолок                                   | Площадь | Стены или перегородки   | Площадь                | Полы   | Площадь |            |
| 110_Техническое помещение                                        |                                           | 6.96    | Грунтовка<br>Плиточный клей – 5 мм<br>Плитка 300х300 – 10 мм<br>от отм 3,00 до отм.: +3.30<br>по типу Окраска стен Текс «Профи»                                | 33<br><br><br>3.30     |   | 6.96    |            |
| 111-Помещение рукомошников                                       | Потолок Армстронг 600х600<br>влагостойкий | 7.56    | от отм 0,00 до отм.: +2.100<br>Грунтовка<br>Плиточный клей – 5 мм<br>Плитка 300х300 – 10 мм<br>от отм 2,10 до отм.: +3.30<br>по типу Окраска стен Текс «Профи» | 23.10<br><br><br>13.20 | Гидроизоляция<br>Плиточный клей – 5 мм<br>Плитка напольная 300х300 – 10 мм                                                         | 7.56    |            |
| 112_Техническое помещение (Построчная с местом для сушки одежды) | Грильято 150х150 серебристый алюминий     | 2.55    | от отм 0,00 до отм.: +2.100<br>Грунтовка<br>Плиточный клей – 5 мм<br>Плитка 300х300 – 10 мм<br>от отм 2,10 до отм.: +3.30<br>по типу Окраска стен Текс «Профи» | 12.60<br><br><br>7.20  | Гидроизоляция<br>Плиточный клей – 5 мм<br>Плитка напольная 300х300 – 10 мм                                                         | 2.55    |            |
| 113 и 114_ Сан узел с тамбуром                                   | Грильято 150х150 серебристый алюминий     | 2.76    | от отм 0,00 до отм.: +2.100<br>Грунтовка<br>Плиточный клей – 5 мм<br>Плитка 300х300 – 10 мм<br>от отм 2,10 до отм.: +3.30<br>по типу Окраска стен Текс «Профи» | 16.80<br><br><br>9.60  | Гидроизоляция<br>Плиточный клей – 5 мм<br>Плитка напольная 300х300 – 10 мм                                                         | 2,78    |            |
| 115_Помещение душевых с тамбуром                                 | Потолок Армстронг 600х600<br>влагостойкий | 20.77   | Грунтовка<br>Плиточный клей – 5 мм<br>Плитка 300х300 – 10 мм                                                                                                   | 112.20                 | Гидроизоляция<br>Плиточный клей – 5 мм<br>Плитка напольная 300х300 – 10 мм<br>Предусмотреть сток воды в канализацию и уклон плитки | 20.77   |            |
| 116_Тренажерный зал                                              | Грильято 150х150 серебристый алюминий     | 58.50   | Окраска стен Текс «Профи»   | 105.60                 | Полиуретановый наливной пол Valspar 0,4                                                                                            | 62,00   |            |
| 117_Коридор                                                      | Грильято 150х150 серебристый алюминий     | 13.90   | Окраска стен Текс «Профи»   | 57.75                  | Полиуретановый наливной пол Valspar 0,4                                                                                            | 13.90   |            |
| 118_Помещение душевых с тамбуром                                 | Потолок Армстронг 600х600<br>влагостойкий | 15.50   | Грунтовка<br>Плиточный клей – 5 мм<br>Плитка 300х300 – 10 мм                                                                                                   | 69.30                  | Гидроизоляция<br>Плиточный клей – 5 мм<br>Плитка напольная 300х300 – 10 мм<br>Предусмотреть сток воды в канализацию и уклон плитки | 15.50   |            |
| 119_Сауна                                                        | Доска вгонка лиственных пород             | 11.14   | Доска вгонка лиственных пород   | 33.75                  | Доска вгонка лиственных пород   | 11.14   |            |

Примечание:

1. По аналогии с данным помещением выполнить помещения рукомошников и сан узлов на всех этажах.

2. Во избежании задрвоения объемов – объемы работ брать из сводной ведомости. объемы по помещению на данном листе даны для ознакомления.

|          |      |      |       |         |      |                                                                                   |                      |      |        |
|----------|------|------|-------|---------|------|-----------------------------------------------------------------------------------|----------------------|------|--------|
|          |      |      |       |         |      | 03-2022/4-AP                                                                      |                      |      |        |
|          |      |      |       |         |      | Капитальный ремонт инженерных систем здания и бытовых помещений ЦРМО РМО отд. №2. |                      |      |        |
| Изм.     | Кол. | Лист | №док. | Подпись | Дата |                                                                                   |                      |      |        |
|          |      |      |       |         |      | Ремонт бытового корпуса                                                           | Стадия               | Лист | Листов |
| ГАП      |      |      |       |         |      |                                                                                   |                      |      |        |
| Н.контр. |      |      |       |         |      | Ведомость отделки помещений первого этажа (продолжение 2/3)                       | ООО “Альянс Энерджи” |      |        |
|          |      |      |       |         |      |                                                                                   |                      |      |        |
|          |      |      |       |         |      |                                                                                   |                      |      |        |

Формат А3



| Ведомость отделки помещений<br>Площадь, м <sup>2</sup> |   |              |                                                              |              |                                         |              |            |
|--------------------------------------------------------|---|--------------|--------------------------------------------------------------|--------------|-----------------------------------------|--------------|------------|
| Наименование или номер помещения                       | Вид отделки элементов интерьера   |              |                                                              |              |                                         |              | Примечание |
|                                                        | Потолок   | Пло-<br>щадь | Стены или перегородки                                        | Пло-<br>щадь | Полы                                    | Пло-<br>щадь |            |
| 120_Комната отдыха                                     | Грильято 150х150 серебристый алюминий   | 16.38        | Окраска стен Текс «Профи»                                    | 105.60       | Полиуретановый наливной пол Valspar 0,4 | 16.38        |            |
| 121_Тамбур                                             | Грильято 150х150 серебристый алюминий   | 6.13         | Окраска стен Текс «Профи»                                    | 26.40        | Полиуретановый наливной пол Valspar 0,4 | 6.13         |            |
| 122_Коридор                                            | Грунтовка запотолочного пространства.<br>Штукатурка запотолочного пространства<br>Грунтовка запотолочного пространства.<br>Окраска запотолочного пространства – краска для стен и потолков Текс «Профи» влагостойкая база А – 2 слоя. | 3.37         | Окраска стен Текс «Профи»                                    | 23.10        | Полиуретановый наливной пол Valspar 0,4 | 3.37         |            |
| 123_Техническое помещение                              | Грунтовка запотолочного пространства.<br>Штукатурка запотолочного пространства<br>Грунтовка запотолочного пространства.<br>Окраска запотолочного пространства – краска для стен и потолков Текс «Профи» влагостойкая                  | 1.08         | Грунтовка<br>Плиточный клей – 5 мм<br>Плитка 300х300 – 10 мм | 11.55        | Полиуретановый наливной пол Valspar 0,4 | 1.08         |            |

Примечание:

1. По аналогии с данным помещением выполнить помещения рукомоЙников и сан узлов на всех этажах.
2. Во избежании задвоения объемов – объемы работ брать из сводной ведомости. объемы по помещению на данном листе даны для ознакомления.

|          |      |      |        |         |      |                                                                                      |                      |      |
|----------|------|------|--------|---------|------|--------------------------------------------------------------------------------------|----------------------|------|
|          |      |      |        |         |      | 03-2022/4-AP                                                                         |                      |      |
|          |      |      |        |         |      | Капитальный ремонт инженерных систем здания и бытовых помещений<br>ЦРМО РМО отд. №2. |                      |      |
| Изм.     | Кол. | Лист | № док. | Подпись | Дата |                                                                                      |                      |      |
|          |      |      |        |         |      | Ремонт бытового корпуса                                                              | Стадия               | Лист |
| ГАП      |      |      |        |         |      |                                                                                      |                      |      |
| Н.контр. |      |      |        |         |      | Ведомость отделки помещений<br>первого этажа<br>(окончание 3/3)                      | ООО "Альянс Энерджи" |      |
|          |      |      |        |         |      |                                                                                      |                      |      |
|          |      |      |        |         |      |                                                                                      |                      |      |

| Ведомость отделки помещений<br>Площадь, м <sup>2</sup> |   |              |   |              |                                                                            |              |            |
|--------------------------------------------------------|---|--------------|---|--------------|----------------------------------------------------------------------------|--------------|------------|
| Наименование или номер помещения                       | Вид отделки элементов интерьера   |              |   |              |                                                                            |              | Примечание |
|                                                        | Потолок   | Пло-<br>щадь | Стены или перегородки   | Пло-<br>щадь | Полы                                                                       | Пло-<br>щадь |            |
| 202_Коридор                                            | Грунтовка запотолочного пространства.<br>Штукатурка запотолочного пространства.<br>Грунтовка запотолочного пространства.<br>Окраска запотолочного пространства – краска для стен и потолков Текс «Профи» влагостойкая база А – 2 слоя.<br>Потолок грильято 150х150 серебристый алюминий (h=50; b=10) ЦСС.<br><br>Далее Тип: Грильято 150х150 серебристый алюминий | 29.91        | Грунтовка<br>Штукатурка<br>Грунтовка<br>Краска для стен и потолков Текс «Профи» влагостойкая база А – 2 слоя.<br><br>Далее Тип: Окраска стен Текс «Профи» | 89.10        | Полиуретановый наливной пол Valspar 0,4                                    | 29.91        |            |
| 203_Кабинет                                            | Грильято 150х150 серебристый алюминий   | 20.23        | Окраска стен Текс «Профи»   | 56.10        | Полиуретановый наливной пол Valspar 0,4                                    | 20.23        |            |
| 204_Кабинет                                            | Грильято 150х150 серебристый алюминий   | 8.71         | Окраска стен Текс «Профи»   | 33.00        | Полиуретановый наливной пол Valspar 0,4                                    | 8.71         |            |
| 205_Сан узел с тамбуром                                | Грильято 150х150 серебристый алюминий   | 3.69         | от отм 0,00 до отм.: +2.100<br>Грунтовка<br>Плиточный клей – 5 мм<br>Плитка 300х300 – 10 мм                                                               | 14.70        | Гидроизоляция<br>Плиточный клей – 5 мм<br>Плитка напольная 300х300 – 10 мм | 3.69         |            |
|                                                        |   |              | от отм 2,10 до отм.: +3.30<br>по типу Окраска стен Текс «Профи»                                                                                           | 8.40         |                                                                            |              |            |
| 206_Сан узел с тамбуром                                | Грильято 150х150 серебристый алюминий   | 3.69         | от отм 0,00 до отм.: +2.100<br>Грунтовка<br>Плиточный клей – 5 мм<br>Плитка 300х300 – 10 мм                                                               | 23.10        | Полиуретановый наливной пол Valspar 0,4                                    | 3.69         |            |
|                                                        |   |              | от отм 2,10 до отм.: +3.30<br>по типу Окраска стен Текс «Профи»                                                                                           | 8.40         |                                                                            |              |            |
| 207_Кабинет                                            | Грильято 150х150 серебристый алюминий   | 50.31        | Окраска стен Текс «Профи»   | 56.70        | Полиуретановый наливной пол Valspar 0,4                                    | 50.31        |            |
| 208_Техническое помещение                              | Грильято 150х150 серебристый алюминий   | 6.91         | от отм 0,00 до отм.: +3.00<br>Грунтовка<br>Плиточный клей – 5 мм<br>Плитка 300х300 – 10 мм                                                                | 31.50        | Гидроизоляция<br>Плиточный клей – 5 мм<br>Плитка напольная 300х300 – 10 мм | 6.91         |            |
|                                                        |   |              | от отм 3,00 до отм.: +3.30<br>по типу Окраска стен Текс «Профи»                                                                                           | 3.15         |                                                                            |              |            |
| 209_Раздевалка мужская                                 | Грильято 150х150 серебристый алюминий   | 66.35        | Окраска стен Текс «Профи»   | 100.00       | Полиуретановый наливной пол Valspar 0,4                                    | 66.35        |            |
| 210_Техническое помещение                              | Грильято 150х150 серебристый алюминий   | 73.91        | Окраска стен Текс «Профи»   | 125.40       | Полиуретановый наливной пол Valspar 0,4                                    | 76.00        |            |
| 211-Помещение<br>рукомойников                          | Потолок Армстронг 600х600<br>влагостойкий   | 7.68         | от отм 0,00 до отм.: +2.100<br>Грунтовка<br>Плиточный клей – 5 мм<br>Плитка 300х300 – 10 мм                                                               | 23.10        | Гидроизоляция<br>Плиточный клей – 5 мм<br>Плитка напольная 300х300 – 10 мм | 7.68         |            |
|                                                        |   |              | от отм 2,10 до отм.: +3.30<br>по типу Окраска стен Текс «Профи»                                                                                           | 13.20        |                                                                            |              |            |

Примечание:

1. По аналогии с данным помещением выполнить помещения рукомойников и сан узлов на всех этажах.
2. Во избежании задвоения объемов – объемы работ брать из сводной ведомости. объемы по помещению на данном листе даны для ознакомления.

|          |      |      |       |         |      |                                                                                   |                      |      |        |
|----------|------|------|-------|---------|------|-----------------------------------------------------------------------------------|----------------------|------|--------|
|          |      |      |       |         |      | 03-2022/4-AP                                                                      |                      |      |        |
|          |      |      |       |         |      | Капитальный ремонт инженерных систем здания и бытовых помещений ЦРМО РМО отд. №2. |                      |      |        |
| Изм.     | Кол. | Лист | №док. | Подпись | Дата |                                                                                   |                      |      |        |
|          |      |      |       |         |      | Ремонт бытового корпуса                                                           | Стадия               | Лист | Листов |
| ГАП      |      |      |       |         |      |                                                                                   |                      |      |        |
| Н.контр. |      |      |       |         |      | Ведомость отделки помещений<br>второго этажа<br>(начало 1/2)                      | ООО "Альянс Энерджи" |      |        |
|          |      |      |       |         |      |                                                                                   |                      |      |        |
|          |      |      |       |         |      |                                                                                   |                      |      |        |

| Ведомость отделки помещений<br>Площадь, м <sup>2</sup>           |                                           |              |                                                                                             |              |   |              |            |
|------------------------------------------------------------------|-------------------------------------------|--------------|---------------------------------------------------------------------------------------------|--------------|---|--------------|------------|
| Наименование или номер помещения                                 | Вид отделки элементов интерьера           |              |                                                                                             |              |   |              | Примечание |
|                                                                  | Потолок                                   | Пло-<br>щадь | Стены или перегородки                                                                       | Пло-<br>щадь | Полы   | Пло-<br>щадь |            |
| 212_Техническое помещение (Построчная с местом для сушки одежды) | Грильято 150х150 серебристый алюминий     | 2.55         | от отм 0,00 до отм.: +2.100<br>Грунтовка<br>Плиточный клей - 5 мм<br>Плитка 300х300 - 10 мм | 12.60        | Гидроизоляция<br>Плиточный клей - 5 мм<br>Плитка напольная 300х300 - 10 мм                                                         | 2.55         |            |
|                                                                  |                                           |              | от отм 2,10 до отм.: +3.30<br>по типу Окраска стен Текс «Профи»                             | 7.20         |   |              |            |
| 213_ Сан узел с тамбуром                                         | Грильято 150х150 серебристый алюминий     | 2.94         | от отм 0,00 до отм.: +2.100<br>Грунтовка<br>Плиточный клей - 5 мм<br>Плитка 300х300 - 10 мм | 16.80        | Гидроизоляция<br>Плиточный клей - 5 мм<br>Плитка напольная 300х300 - 10 мм                                                         | 2,94         |            |
|                                                                  |                                           |              | от отм 2,10 до отм.: +3.30<br>по типу Окраска стен Текс «Профи»                             | 9.60         |   |              |            |
| 214_Тамбур душевой                                               | Потолок Армстронг 600х600<br>влагостойкий | 5.76         | Грунтовка<br>Плиточный клей - 5 мм<br>Плитка 300х300 - 10 мм                                | 112.20       | Гидроизоляция<br>Плиточный клей - 5 мм<br>Плитка напольная 300х300 - 10 мм                                                         | 5.76         |            |
| 215_Душевые                                                      | Потолок Армстронг 600х600<br>влагостойкий | 25.11        | Грунтовка<br>Плиточный клей - 5 мм<br>Плитка 300х300 - 10 мм                                | 125.40       | Гидроизоляция<br>Плиточный клей - 5 мм<br>Плитка напольная 300х300 - 10 мм<br>Предусмотреть сток воды в канализацию и уклон плитки | 25,11        |            |
| 216_Раздевалка мужская                                           | Грильято 150х150 серебристый алюминий     | 100.98       | Окраска стен Текс «Профи»                                                                   | 145.20       | Полиуретановый наливной пол Valspar 0,4                                                                                            | 100.98       |            |
| 217_Тамбур душевой                                               | Потолок Армстронг 600х600<br>влагостойкий | 5.76         | Грунтовка<br>Плиточный клей - 5 мм<br>Плитка 300х300 - 10 мм                                | 112.20       | Гидроизоляция<br>Плиточный клей - 5 мм<br>Плитка напольная 300х300 - 10 мм                                                         | 5.76         |            |
| 218_Коридор                                                      | Грильято 150х150 серебристый алюминий     | 7.49         | Окраска стен Текс «Профи»                                                                   | 27.00        | Полиуретановый наливной пол Valspar 0,4                                                                                            | 7.49         |            |
| 219_Кабинет                                                      | Грильято 150х150 серебристый алюминий     | 9.92         | Окраска стен Текс «Профи»                                                                   | 36.30        | Полиуретановый наливной пол Valspar 0,4                                                                                            | 9.92         |            |

Примечание:

1. По аналогии с данным помещением выполнить помещения рукомоЙников и сан узлов на всех этажах.
2. Во избежании задвоения объемов – объемы работ брать из сводной ведомости. объемы по помещению на данном листе даны для ознакомления.

|                 |      |      |       |         |      |                                                                                      |                      |        |
|-----------------|------|------|-------|---------|------|--------------------------------------------------------------------------------------|----------------------|--------|
|                 |      |      |       |         |      | _____ -АР                                                                            |                      |        |
|                 |      |      |       |         |      | Капитальный ремонт инженерных систем здания и бытовых помещений<br>ЦРМО РМО отд. №2. |                      |        |
| Изм.            | Кол. | Лист | №док. | Подпись | Дата |                                                                                      |                      |        |
|                 |      |      |       |         |      | Ремонт бытового корпуса                                                              | Стадия               | Лист   |
| ГАП<br>Н.контр. |      |      |       |         |      |                                                                                      |                      | Листов |
|                 |      |      |       |         |      | Ведомость отделки помещений<br>второго этажа<br>(окончание 2/2)                      | ООО “Альянс Энерджи” |        |
|                 |      |      |       |         |      |                                                                                      |                      |        |

| <div>Ведомость отделки помещений</div> <div>Площадь, м<sup>2</sup></div> |   |         |   |         |                                                                            |         |            |
|--------------------------------------------------------------------------|---|---------|---|---------|----------------------------------------------------------------------------|---------|------------|
| Наименование или номер помещения                                         | Вид отделки элементов интерьера   |         |   |         |                                                                            |         | Примечание |
|                                                                          | Потолок   | Площадь | Стены или перегородки   | Площадь | Полы                                                                       | Площадь |            |
| 302_Коридор                                                              | Грунтовка запотолочного пространства.<br>Штукатурка запотолочного пространства.<br>Грунтовка запотолочного пространства.<br>Окраска запотолочного пространства – краска для стен и потолков Текс «Профи» влагостойкая база А – 2 слоя.<br>Потолок грильято 150х150 серебристый алюминий (h=50; b=10) ЦСС.<br><br>Далее Тип: Грильято 150х150 серебристый алюминий | 29.91   | Грунтовка<br>Штукатурка<br>Грунтовка<br>Краска для стен и потолков Текс «Профи» влагостойкая база А – 2 слоя.<br><br>Далее Тип: Окраска стен Текс «Профи» | 89.10   | Полиуретановый наливной пол Valspar 0,4                                    | 29.91   |            |
| 303_Кабинет                                                              | Грильято 150х150 серебристый алюминий   | 20.23   | Окраска стен Текс «Профи»   | 56.10   | Полиуретановый наливной пол Valspar 0,4                                    | 20.23   |            |
| 304_Кабинет                                                              | Грильято 150х150 серебристый алюминий   | 8.71    | Окраска стен Текс «Профи»   | 33.00   | Полиуретановый наливной пол Valspar 0,4                                    | 8.71    |            |
| 305_Сан узел с тамбуром                                                  | Грильято 150х150 серебристый алюминий   | 3.69    | от отм 0,00 до отм.: +2.100<br>Грунтовка<br>Плиточный клей – 5 мм<br>Плитка 300х300 – 10 мм                                                               | 14.70   | Гидроизоляция<br>Плиточный клей – 5 мм<br>Плитка напольная 300х300 – 10 мм | 3.69    |            |
|                                                                          |   |         | от отм 2,10 до отм.: +3.30<br>по типу Окраска стен Текс «Профи»                                                                                           | 8.40    |                                                                            |         |            |
| 306_Сан узел с тамбуром                                                  | Грильято 150х150 серебристый алюминий   | 3.69    | от отм 0,00 до отм.: +2.100<br>Грунтовка<br>Плиточный клей – 5 мм<br>Плитка 300х300 – 10 мм                                                               | 23.10   | Полиуретановый наливной пол Valspar 0,4                                    | 3.69    |            |
|                                                                          |   |         | от отм 2,10 до отм.: +3.30<br>по типу Окраска стен Текс «Профи»                                                                                           | 8.40    |                                                                            |         |            |
| 307_Кабинет                                                              | Грильято 150х150 серебристый алюминий   | 16.38   | Окраска стен Текс «Профи»   | 52.80   | Полиуретановый наливной пол Valspar 0,4                                    | 16.38   |            |
| 307a_Кабинет                                                             | Грильято 150х150 серебристый алюминий   | 16.38   | Окраска стен Текс «Профи»   | 52.80   | Полиуретановый наливной пол Valspar 0,4                                    | 16.38   |            |
| 307б_Кабинет                                                             | Грильято 150х150 серебристый алюминий   | 32.93   | Окраска стен Текс «Профи»   | 72.60   | Полиуретановый наливной пол Valspar 0,4                                    | 32.93   |            |
| 308_Техническое помещение                                                | Грильято 150х150 серебристый алюминий   | 6.91    | от отм 0,00 до отм.: +3.00<br>Грунтовка<br>Плиточный клей – 5 мм<br>Плитка 300х300 – 10 мм                                                                | 31.50   | Гидроизоляция<br>Плиточный клей – 5 мм<br>Плитка напольная 300х300 – 10 мм | 6.91    |            |
|                                                                          |   |         | от отм 3,00 до отм.: +3.30<br>по типу Окраска стен Текс «Профи»                                                                                           | 3.15    |                                                                            |         |            |
| 309_Раздевалка мужская                                                   | Грильято 150х150 серебристый алюминий   | 49.13   | Окраска стен Текс «Профи»   | 95.70   | Полиуретановый наливной пол Valspar 0,4                                    | 49.13   |            |
| 310_Техническое помещение                                                | Грильято 150х150 серебристый алюминий   | 73.91   | Окраска стен Текс «Профи»   | 125.40  | Полиуретановый наливной пол Valspar 0,4                                    | 76.00   |            |

|   |                 |      |      |       |         |      |                                                                                   |                      |      |        |
|---|-----------------|------|------|-------|---------|------|-----------------------------------------------------------------------------------|----------------------|------|--------|
| <div>Примечание:</div> <div>1. По аналогии с данным помещением выполнить помещения рукомоЙников и сан узлов на всех этажах.</div> <div>2. Во избежании задвоения объемов – объемы работ брать из сводной ведомости. объемы по помещению на данном листе даны для ознакомления.</div> |                 |      |      |       |         |      | 03-2022/4-AP                                                                      |                      |      |        |
|   |                 |      |      |       |         |      | Капитальный ремонт инженерных систем здания и бытовых помещений ЦРМО РМО отд. №2. |                      |      |        |
|   | Изм.            | Кол. | Лист | №док. | Подпись | Дата |                                                                                   |                      |      |        |
|   |                 |      |      |       |         |      | Ремонт бытового корпуса                                                           | Стадия               | Лист | Листов |
|   | ГАП<br>Н.контр. |      |      |       |         |      |                                                                                   |                      |      |        |
|   |                 |      |      |       |         |      | Ведомость отделки помещений<br>третьего этажа<br>(начало 1/2)                     | ООО “Альянс Энерджи” |      |        |
|   |                 |      |      |       |         |      |                                                                                   |                      |      |        |
| Ведомость отделки помещений<br>Площадь, м <sup>2</sup>                    |                                           |              |                                                                                             |              |   |              |            |
|---------------------------------------------------------------------------|-------------------------------------------|--------------|---------------------------------------------------------------------------------------------|--------------|---|--------------|------------|
| Наименование или номер помещения                                          | Вид отделки элементов интерьера           |              |                                                                                             |              |   |              | Примечание |
|                                                                           | Потолок                                   | Пло-<br>щадь | Стены или перегородки                                                                       | Пло-<br>щадь | Полы   | Пло-<br>щадь |            |
| 311-Помещение<br>рукомойников                                             | Потолок Армстронг 600х600<br>влагостойкий | 7.68         | от отм 0,00 до отм.: +2.100<br>Грунтовка<br>Плиточный клей - 5 мм<br>Плитка 300х300 - 10 мм | 23.10        | Гидроизоляция<br>Плиточный клей - 5 мм<br>Плитка напольная 300х300 - 10 мм                                                            | 7.68         |            |
|                                                                           |                                           |              | от отм 2,10 до отм.: +3.30<br>по типу Окраска стен Текс «Профи»                             | 13.20        |   |              |            |
| 312_Техническое<br>помещение (Построчная с<br>местом для сушки<br>одежды) | Грильято 150х150 серебристый алюминий     | 2.55         | от отм 0,00 до отм.: +2.100<br>Грунтовка<br>Плиточный клей - 5 мм<br>Плитка 300х300 - 10 мм | 12.60        | Гидроизоляция<br>Плиточный клей - 5 мм<br>Плитка напольная 300х300 - 10 мм                                                            | 2.55         |            |
|                                                                           |                                           |              | от отм 2,10 до отм.: +3.30<br>по типу Окраска стен Текс «Профи»                             | 7.20         |   |              |            |
| 313_ Сан узел с<br>тамбуром                                               | Грильято 150х150 серебристый алюминий     | 2.94         | от отм 0,00 до отм.: +2.100<br>Грунтовка<br>Плиточный клей - 5 мм<br>Плитка 300х300 - 10 мм | 16.80        | Гидроизоляция<br>Плиточный клей - 5 мм<br>Плитка напольная 300х300 - 10 мм                                                            | 2.94         |            |
|                                                                           |                                           |              | от отм 2,10 до отм.: +3.30<br>по типу Окраска стен Текс «Профи»                             | 9.60         |   |              |            |
| 314_Тамбур душевой                                                        | Потолок Армстронг 600х600<br>влагостойкий | 5.76         | Грунтовка<br>Плиточный клей - 5 мм<br>Плитка 300х300 - 10 мм                                | 112.20       | Гидроизоляция<br>Плиточный клей - 5 мм<br>Плитка напольная 300х300 - 10 мм                                                            | 5.76         |            |
| 315_Душевые                                                               | Потолок Армстронг 600х600<br>влагостойкий | 25.11        | Грунтовка<br>Плиточный клей - 5 мм<br>Плитка 300х300 - 10 мм                                | 125.40       | Гидроизоляция<br>Плиточный клей - 5 мм<br>Плитка напольная 300х300 - 10 мм<br>Предусмотреть сток воды в канализацию и<br>уклон плитки | 25.11        |            |
| 316_Раздевалка мужская                                                    | Грильято 150х150 серебристый алюминий     | 100.98       | Окраска стен Текс «Профи»                                                                   | 145.20       | Полиуретановый наливной пол Valspar 0,4                                                                                               | 100.98       |            |
| 317_Тамбур душевой                                                        | Потолок Армстронг 600х600<br>влагостойкий | 5.76         | Грунтовка<br>Плиточный клей - 5 мм<br>Плитка 300х300 - 10 мм                                | 112.20       | Гидроизоляция<br>Плиточный клей - 5 мм<br>Плитка напольная 300х300 - 10 мм                                                            | 5.76         |            |
| 318_Коридор                                                               | Грильято 150х150 серебристый алюминий     | 7.49         | Окраска стен Текс «Профи»                                                                   | 27.00        | Полиуретановый наливной пол Valspar 0,4                                                                                               | 7.49         |            |
| 319_Кабинет                                                               | Грильято 150х150 серебристый алюминий     | 9.92         | Окраска стен Текс «Профи»                                                                   | 36.30        | Полиуретановый наливной пол Valspar 0,4                                                                                               | 9.92         |            |

Примечание:

- По аналогии с данным помещением выполнить помещения рукомойников и сан узлов на всех этажах.
- Во избежании задвоения объемов – объемы работ брать из сводной ведомости. объемы по помещению на данном листе даны для ознакомления.

|          |      |      |       |         |      |                                                                                   |                      |      |
|----------|------|------|-------|---------|------|-----------------------------------------------------------------------------------|----------------------|------|
|          |      |      |       |         |      | 03-2022/4-AP                                                                      |                      |      |
|          |      |      |       |         |      | Капитальный ремонт инженерных систем здания и бытовых помещений ЦРМО РМО отд. №2. |                      |      |
| Изм.     | Кол. | Лист | №док. | Подпись | Дата |                                                                                   |                      |      |
|          |      |      |       |         |      | Ремонт бытового корпуса                                                           | Стадия               | Лист |
| ГАП      |      |      |       |         |      |                                                                                   |                      |      |
| Н.контр. |      |      |       |         |      | Ведомость отделки помещений<br>третьего этажа<br>(окончание 2/2)                  | ООО "Альянс Энерджи" |      |
|          |      |      |       |         |      |                                                                                   |                      |      |
|          |      |      |       |         |      |                                                                                   |                      |      |

Ведомость отделки помещений

Площадь, м²

| Наименование или номер помещения | Вид отделки элементов интерьера   |         |   |         |                                                                            |         | Примечание |
|----------------------------------|---|---------|---|---------|----------------------------------------------------------------------------|---------|------------|
|                                  | Потолок   | Площадь | Стены или перегородки   | Площадь | Полы                                                                       | Площадь |            |
| 402_Коридор                      | Грунтовка запотолочного пространства.<br>Окраска запотолочного пространства – краска для стен и потолков Текс «Профи» влагостойкая база А – 2 слоя.<br>Потолок грильято 150х150 серебристый алюминий (h=50; b=10) ЦСС.<br><br>Далее Тип: Грильято 150х150 серебристый алюминий | 29.91   | Грунтовка<br>Краска для стен и потолков Текс «Профи» влагостойкая база А – 2 слоя.<br><br>Далее Тип: Окраска стен Текс «Профи» | 89.10   |                                                                            | 29.91   |            |
| 403_Кабинет                      | Грильято 150х150 серебристый алюминий   | 20.23   | Окраска стен Текс «Профи»   | 56.10   | Полиуретановый наливной пол Valspar 0,4                                    | 20.23   |            |
| 404_Кабинет                      | Грильято 150х150 серебристый алюминий   | 8.71    | Окраска стен Текс «Профи»   | 33.00   | Полиуретановый наливной пол Valspar 0,4                                    | 8.71    |            |
| 405_Сан узел с тамбуром          | Грильято 150х150 серебристый алюминий   | 3.69    | от отм 0,00 до отм.: +2.100<br>Грунтовка<br>Плиточный клей – 5 мм<br>Плитка 300х300 – 10 мм                                    | 14.70   | Гидроизоляция<br>Плиточный клей – 5 мм<br>Плитка напольная 300х300 – 10 мм | 3.69    |            |
|                                  |   |         | от отм 2,10 до отм.: +3.30<br>по типу Окраска стен Текс «Профи»                                                                | 8.40    |                                                                            |         |            |
| 406_Сан узел с тамбуром          | Грильято 150х150 серебристый алюминий   | 3.69    | от отм 0,00 до отм.: +2.100<br>Грунтовка<br>Плиточный клей – 5 мм<br>Плитка 300х300 – 10 мм                                    | 23.10   | Полиуретановый наливной пол Valspar 0,4                                    | 3.69    |            |
|                                  |   |         | от отм 2,10 до отм.: +3.30<br>по типу Окраска стен Текс «Профи»                                                                | 8.40    |                                                                            |         |            |
| 407_Кабинет                      | Грильято 150х150 серебристый алюминий   | 16.38   | Окраска стен Текс «Профи»   | 52.80   | Полиуретановый наливной пол Valspar 0,4                                    | 16.38   |            |
| 407a_Кабинет                     | Грильято 150х150 серебристый алюминий   | 16.38   | Окраска стен Текс «Профи»   | 52.80   | Полиуретановый наливной пол Valspar 0,4                                    | 16.38   |            |
| 407б_Кабинет                     | Грильято 150х150 серебристый алюминий   | 16.38   | Окраска стен Текс «Профи»   | 52.80   | Полиуретановый наливной пол Valspar 0,4                                    | 16.38   |            |
| 408_Техническое помещение        | Грильято 150х150 серебристый алюминий   | 6.91    | от отм 0,00 до отм.: +3.00<br>Грунтовка<br>Плиточный клей – 5 мм<br>Плитка 300х300 – 10 мм                                     | 31.50   | Гидроизоляция<br>Плиточный клей – 5 мм<br>Плитка напольная 300х300 – 10 мм | 6.91    |            |
|                                  |   |         | от отм 3,00 до отм.: +3.30<br>по типу Окраска стен Текс «Профи»                                                                | 3.15    |                                                                            |         |            |
| 409_Раздевалка мужская           | Грильято 150х150 серебристый алюминий   | 66.35   | Окраска стен Текс «Профи»   | 100.00  | Полиуретановый наливной пол Valspar 0,4                                    | 66.35   |            |
| 410_Техническое помещение        | Грильято 150х150 серебристый алюминий   | 73.91   | Окраска стен Текс «Профи»   | 125.40  | Полиуретановый наливной пол Valspar 0,4                                    | 76.00   |            |
| 411-Помещение<br>рукомойников    | Потолок Армстронг 600х600<br>влагостойкий   | 7.68    | от отм 0,00 до отм.: +2.100<br>Грунтовка<br>Плиточный клей – 5 мм<br>Плитка 300х300 – 10 мм                                    | 23.10   | Гидроизоляция<br>Плиточный клей – 5 мм<br>Плитка напольная 300х300 – 10 мм | 7.68    |            |
|                                  |   |         | от отм 2,10 до отм.: +3.30<br>по типу Окраска стен Текс «Профи»                                                                | 13.20   |                                                                            |         |            |

Примечание:

1.

По аналогии с данным помещением выполнить помещения рукомойников и сан узлов на всех этажах.
2.

Во избежании удвоения объемов – объемы работ брать из сводной ведомости. объемы по помещению на данном листе даны для ознакомления.

|          |      |      |       |         |      |                                                                                   |                      |      |        |
|----------|------|------|-------|---------|------|-----------------------------------------------------------------------------------|----------------------|------|--------|
|          |      |      |       |         |      | 03-2022/4-AP                                                                      |                      |      |        |
|          |      |      |       |         |      | Капитальный ремонт инженерных систем здания и бытовых помещений ЦРМО РМО отд. №2. |                      |      |        |
|          |      |      |       |         |      |                                                                                   |                      |      |        |
| Изм.     | Кол. | Лист | №док. | Подпись | Дата | Ремонт бытового корпуса                                                           | Стадия               | Лист | Листов |
| ГАП      |      |      |       |         |      |                                                                                   |                      |      |        |
| Н.контр. |      |      |       |         |      |                                                                                   |                      |      |        |
|          |      |      |       |         |      | Ведомость отделки помещений четвертого этажа (начало 1/2)                         | ООО "Альянс Энерджи" |      |        |

| Ведомость отделки помещений<br>Площадь, м <sup>2</sup>           |                                           |              |                                                                                             |              |   |              |            |
|------------------------------------------------------------------|-------------------------------------------|--------------|---------------------------------------------------------------------------------------------|--------------|---|--------------|------------|
| Наименование или номер помещения                                 | Вид отделки элементов интерьера           |              |                                                                                             |              |   |              | Примечание |
|                                                                  | Потолок                                   | Пло-<br>щадь | Стены или перегородки                                                                       | Пло-<br>щадь | Полы   | Пло-<br>щадь |            |
| 412_Техническое помещение (Построчная с местом для сушки одежды) | Грильято 150х150 серебристый алюминий     | 2.55         | от отм 0,00 до отм.: +2.100<br>Грунтовка<br>Плиточный клей - 5 мм<br>Плитка 300х300 - 10 мм | 12.60        | Гидроизоляция<br>Плиточный клей - 5 мм<br>Плитка напольная 300х300 - 10 мм                                                         | 2.55         |            |
|                                                                  |                                           |              | от отм 2,10 до отм.: +3.30<br>по типу Окраска стен Текс «Профи»                             | 7.20         |   |              |            |
| 413_ Сан узел с тамбуром                                         | Грильято 150х150 серебристый алюминий     | 2.94         | от отм 0,00 до отм.: +2.100<br>Грунтовка<br>Плиточный клей - 5 мм<br>Плитка 300х300 - 10 мм | 16.80        | Гидроизоляция<br>Плиточный клей - 5 мм<br>Плитка напольная 300х300 - 10 мм                                                         | 2,94         |            |
|                                                                  |                                           |              | от отм 2,10 до отм.: +3.30<br>по типу Окраска стен Текс «Профи»                             | 9.60         |   |              |            |
| 414_Тамбур душевой                                               | Потолок Армстронг 600х600<br>влагостойкий | 5.76         | Грунтовка<br>Плиточный клей - 5 мм<br>Плитка 300х300 - 10 мм                                | 112.20       | Гидроизоляция<br>Плиточный клей - 5 мм<br>Плитка напольная 300х300 - 10 мм                                                         | 5.76         |            |
| 415_Душевые                                                      | Потолок Армстронг 600х600<br>влагостойкий | 25.11        | Грунтовка<br>Плиточный клей - 5 мм<br>Плитка 300х300 - 10 мм                                | 125.40       | Гидроизоляция<br>Плиточный клей - 5 мм<br>Плитка напольная 300х300 - 10 мм<br>Предусмотреть сток воды в канализацию и уклон плитки | 25,11        |            |
| 416_Раздевалка мужская                                           | Грильято 150х150 серебристый алюминий     | 100.98       | Окраска стен Текс «Профи»                                                                   | 145.20       | Полиуретановый наливной пол Valspar 0,4                                                                                            | 100.98       |            |
| 417_Тамбур душевой                                               | Потолок Армстронг 600х600<br>влагостойкий | 5.76         | Грунтовка<br>Плиточный клей - 5 мм<br>Плитка 300х300 - 10 мм                                | 112.20       | Гидроизоляция<br>Плиточный клей - 5 мм<br>Плитка напольная 300х300 - 10 мм                                                         | 5.76         |            |
| 418_Коридор                                                      | Грильято 150х150 серебристый алюминий     | 7.49         | Окраска стен Текс «Профи»                                                                   | 27.00        | Полиуретановый наливной пол Valspar 0,4                                                                                            | 7.49         |            |
| 419_Кабинет                                                      | Грильято 150х150 серебристый алюминий     | 9.92         | Окраска стен Текс «Профи»                                                                   | 36.30        | Полиуретановый наливной пол Valspar 0,4                                                                                            | 9.92         |            |

Примечание:

1. По аналогии с данным помещением выполнить помещения рукомоЙников и сан узлов на всех этажах.
2. Во избежании задвоения объемов – объемы работ брать из сводной ведомости. объемы по помещению на данном листе даны для ознакомления.

|                 |      |      |       |         |      |                                                                                   |                      |      |
|-----------------|------|------|-------|---------|------|-----------------------------------------------------------------------------------|----------------------|------|
|                 |      |      |       |         |      | 03-2022/4-AP                                                                      |                      |      |
|                 |      |      |       |         |      | Капитальный ремонт инженерных систем здания и бытовых помещений ЦРМО РМО отд. №2. |                      |      |
| Изм.            | Кол. | Лист | №док. | Подпись | Дата |                                                                                   |                      |      |
|                 |      |      |       |         |      | Ремонт бытового корпуса                                                           | Стадия               | Лист |
| ГАП<br>Н.контр. |      |      |       |         |      |                                                                                   |                      |      |
|                 |      |      |       |         |      | Ведомость отделки помещений четвертого этажа (начало 1/2)                         | ООО "Альянс Энерджи" |      |
|                 |      |      |       |         |      |                                                                                   |                      |      |



|            |          |           |        |         |      |                                                                                   |                      |      |        |
|------------|----------|-----------|--------|---------|------|-----------------------------------------------------------------------------------|----------------------|------|--------|
|            |          |           |        |         |      | 03-2022/4 - АР                                                                    |                      |      |        |
|            |          |           |        |         |      | Капитальный ремонт инженерных систем здания и бытовых помещений ЦРМО РМО отд. №2. |                      |      |        |
|            |          |           |        |         |      |                                                                                   |                      |      |        |
| Изм.       | Кол. уч. | Лист      | № док. | Подпись | Дата |                                                                                   |                      |      |        |
| Разработал |          | Несмиянов |        |         |      | Эскизный проект                                                                   | Стадия               | Лист | Листов |
| ГИП        |          | Олексенко |        |         |      |                                                                                   | Р                    | 20   |        |
|            |          |           |        |         |      | Визуализации                                                                      | ООО "Альянс Энерджи" |      |        |
| Н. контр.  |          | Злобин    |        |         |      |                                                                                   |                      |      |        |
|            |          |           |        |         |      |                                                                                   |                      |      |        |

|              |              |  |              |  |  |
|--------------|--------------|--|--------------|--|--|
| Согласовано  |              |  |              |  |  |
|              |              |  |              |  |  |
|              |              |  |              |  |  |
| Име. № подл. | Подп. и дата |  | Взам. име. № |  |  |
|              |              |  |              |  |  |
|              |              |  |              |  |  |